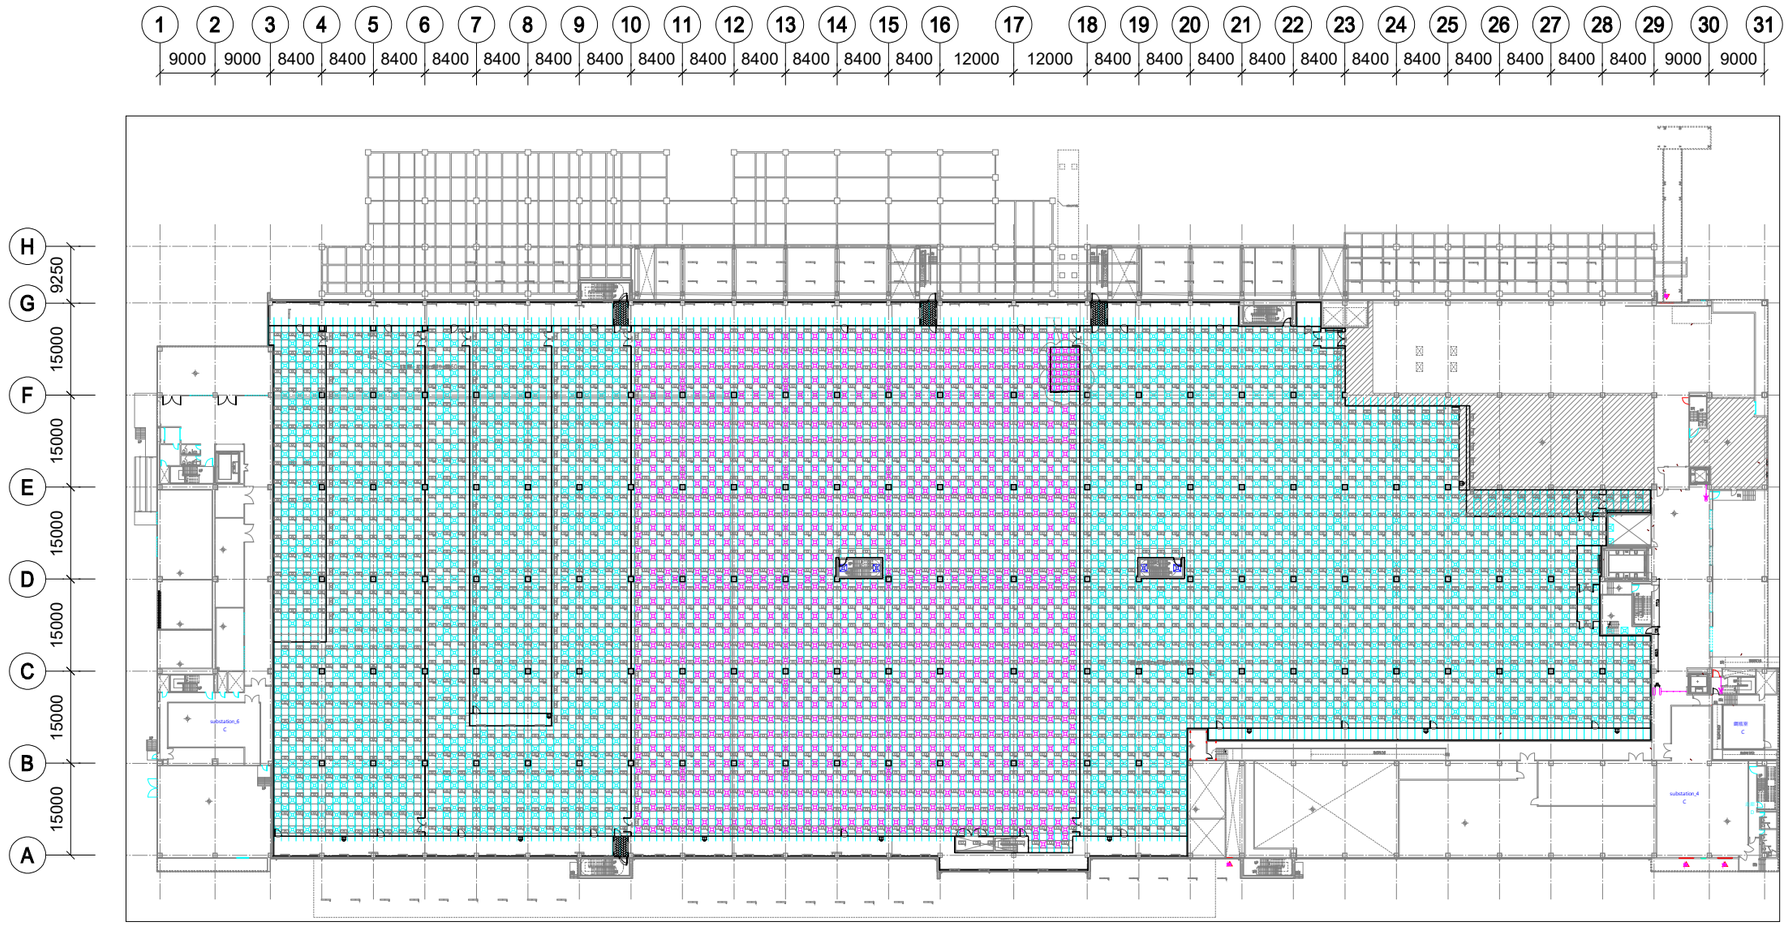


CEILING SYMBOL & LEGEND (F10)	
SYMBOL	DESCRIPTION
	1136mm x 1136mm FFU ,PTFE
	1136mm x 1136mm FFU ,PTFE+化學濾網
	1136mm x 536mm FFU ,PTFE+化學濾網
	1136mm x 1136mm FFU, HEPA

OWNER / DEVELOPER

micron

ARCHITECTURAL CONSULTANT

QUO 陳昆豐建築師事務所

CIVIL & STRUCTURAL CONSULTANT

禾森工程顧問有限公司

MECHANICAL & ELECTRICAL CONSULTANT & CONTRACTOR

YKE 洋基工程股份有限公司 YANKEY Engineering Co.,Ltd

SUB-CONTRACTOR

PROJECT ADDRESS

KEY PLAN

REV	DATE	DESCRIPTION	ISSUED BY
Revisions			

PROJECT TITLE

美光台南廠188K增建工程

MECH

PROJECT PHASE

Concept Design

DRAWING TITLE

DE_MMTN_F2_B002_B_FUDC_2L15

F2 L15 風機過濾機組平面配置圖

S-Fab L15 FFU LAYOUT

DESIGNED : DRAWN : CHECKED :

DATE : **2025/07/23** JOB NO. : SCALE : **A3:1/1000**

DRAWING NO. REV

DE_MMTN_F2_B002_B_FUDC_2L15 **A**

[SHEET PURPOSE] SHEET: SIZE