


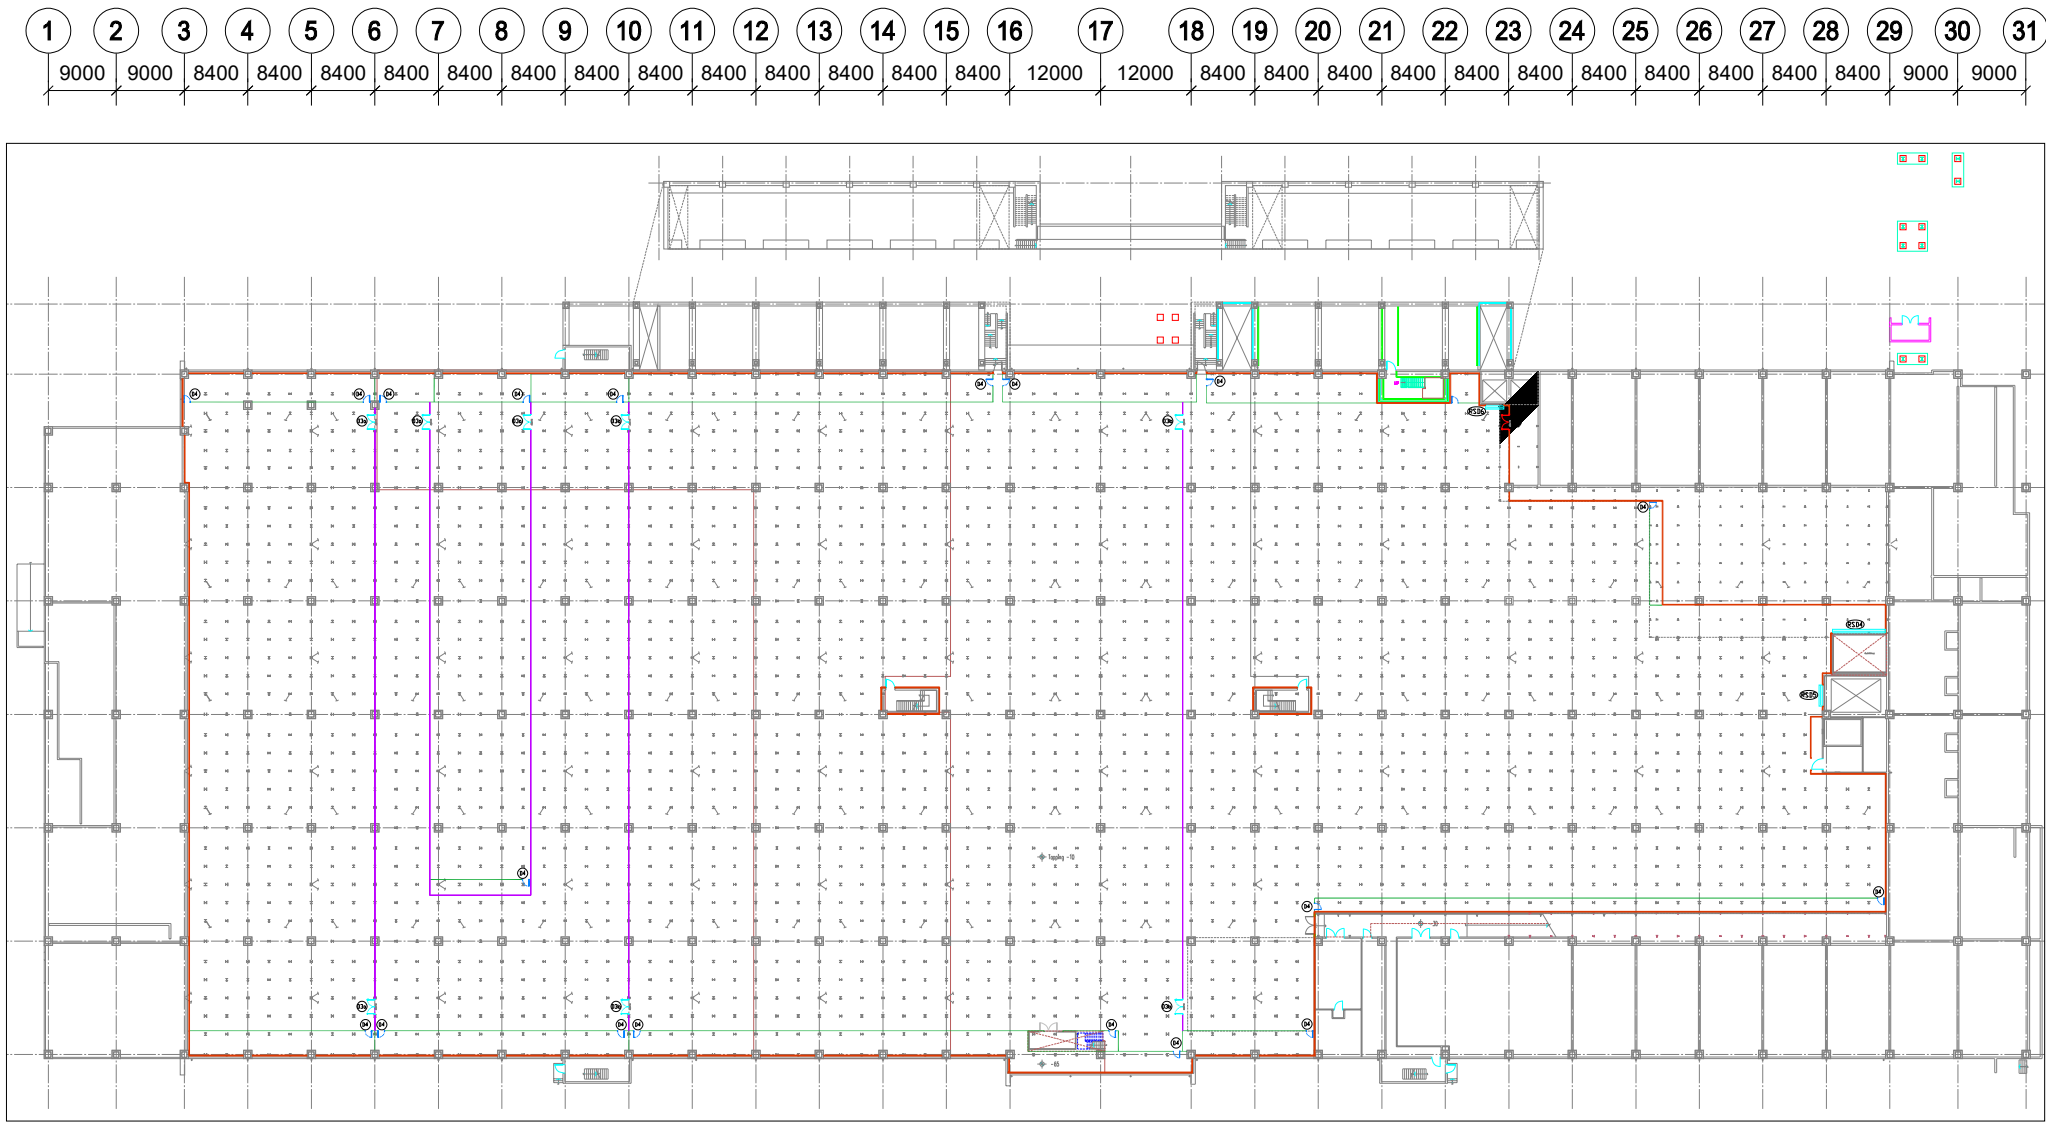

MATERIAL	SYMBOL
鋁鍍金庫板隔間 (t=50mm) 非抗靜電 H=3500mm	
鋁鍍金庫板隔間 (t=50mm) 雙面抗靜電 H=4200mm	
鋁鍍金庫板隔間 (t=50mm) 單面抗靜電 H=4200mm	
鋁鍍金庫板隔間 (t=50mm) 單面抗靜電 H=3000mm	
防火二小時岩棉庫板隔間 (t=100mm) 非抗靜電 H=3500mm	
防火二小時岩棉庫板隔間 (t=100mm) 非抗靜電 H=7500mm	
防火二小時岩棉庫板隔間 (t=100mm) 單面抗靜電 H=7500mm	
DIVIDER H=3500mm	
DIVIDER H=7500mm	
庫面 / 門框 (FL+1500mm 防刮牆白鐵牆面 t=1.0mm) 註: RT 高架地板完整面起算, 庫板寬度為1200mm.	

DOOR SYMBOL & LEGEND		
編號	SYMBOL	DESCRIPTION (含門框尺寸)
D1a		單開庫板門 1200W x 2400H 附視窗(白光)
D1b		單開庫板門 1200W x 2400H 附視窗(黃光)
D1c		單開庫板門 1200W x 2400H 把手型 圓形拉環鎖
D2a		雙開庫板門 2400W x 2400H 附視窗(白光)
D2b		雙開庫板門 2400W x 2400H 附視窗(黃光)
D3a		雙開庫板門 2000W x 1700H 附視窗(白光)
D3b		雙開庫板門 2000W x 1700H 附視窗(黃光)
D4		單開鋼板門 900W x 1700H 風門牆 (鐵皮上開門, 須氣密)
F D1		二小時雙開防火門 2400W x 2400H
F D2		二小時雙開防火門 2000W x 1700H
AS D1		單開自動門 1200W x 2400H 附視窗(白光)
FS D1		二小時鐵捲門 7000W x 3000H (馬達須防蟻)
FS D2		二小時鐵捲門 2800W x 3000H (馬達須防蟻)
FS D3		二小時鐵捲門 2400W x 3000H (馬達須防蟻)
FS D4		二小時鐵捲門 7000W x 1700H (馬達須防蟻)
FS D5		二小時鐵捲門 2800W x 1700H (馬達須防蟻)
FS D6		二小時鐵捲門 2400W x 1700H (馬達須防蟻)

EQUIPMENT SYMBOL & LEGEND		
SYMBOL	DESCRIPTION 單位:mm	REMARKS
	爬梯(STAINLESS STEEL)	LAD

OWNER / DEVELOPER

ARCHITECTURAL CONSULTANT

QUO 陳昆豐建築師事務所

CIVIL & STRUCTURAL CONSULTANT

禾森工程顧問有限公司

MECHANICAL & ELECTRICAL CONSULTANT & CONTRACTOR

洋基工程股份有限公司
YANKEY Engineering Co.,Ltd

SUB-CONTRACTOR

PROJECT ADDRESS

KEY PLAN

PROJECT TITLE

美光台南廠188K增建工程

PROJECT PHASE

MECH
Concept Design

DRAWING TITLE

DE_MMTN_F2_B002_B_PRTN_2L05
F2 L05 隔間平面配置圖
S-Fab L05 PA LAYOUT

DESIGNED: DATE: 2025/08/17

DRAWN: JOB NO.:

CHECKED: SCALE: A3:1/1000

DRAWING NO. DE_MMTN_F2_B002_B_PRTN_2L05

REV A

SHEET PURPOSE

ISSUED BY

SIZE