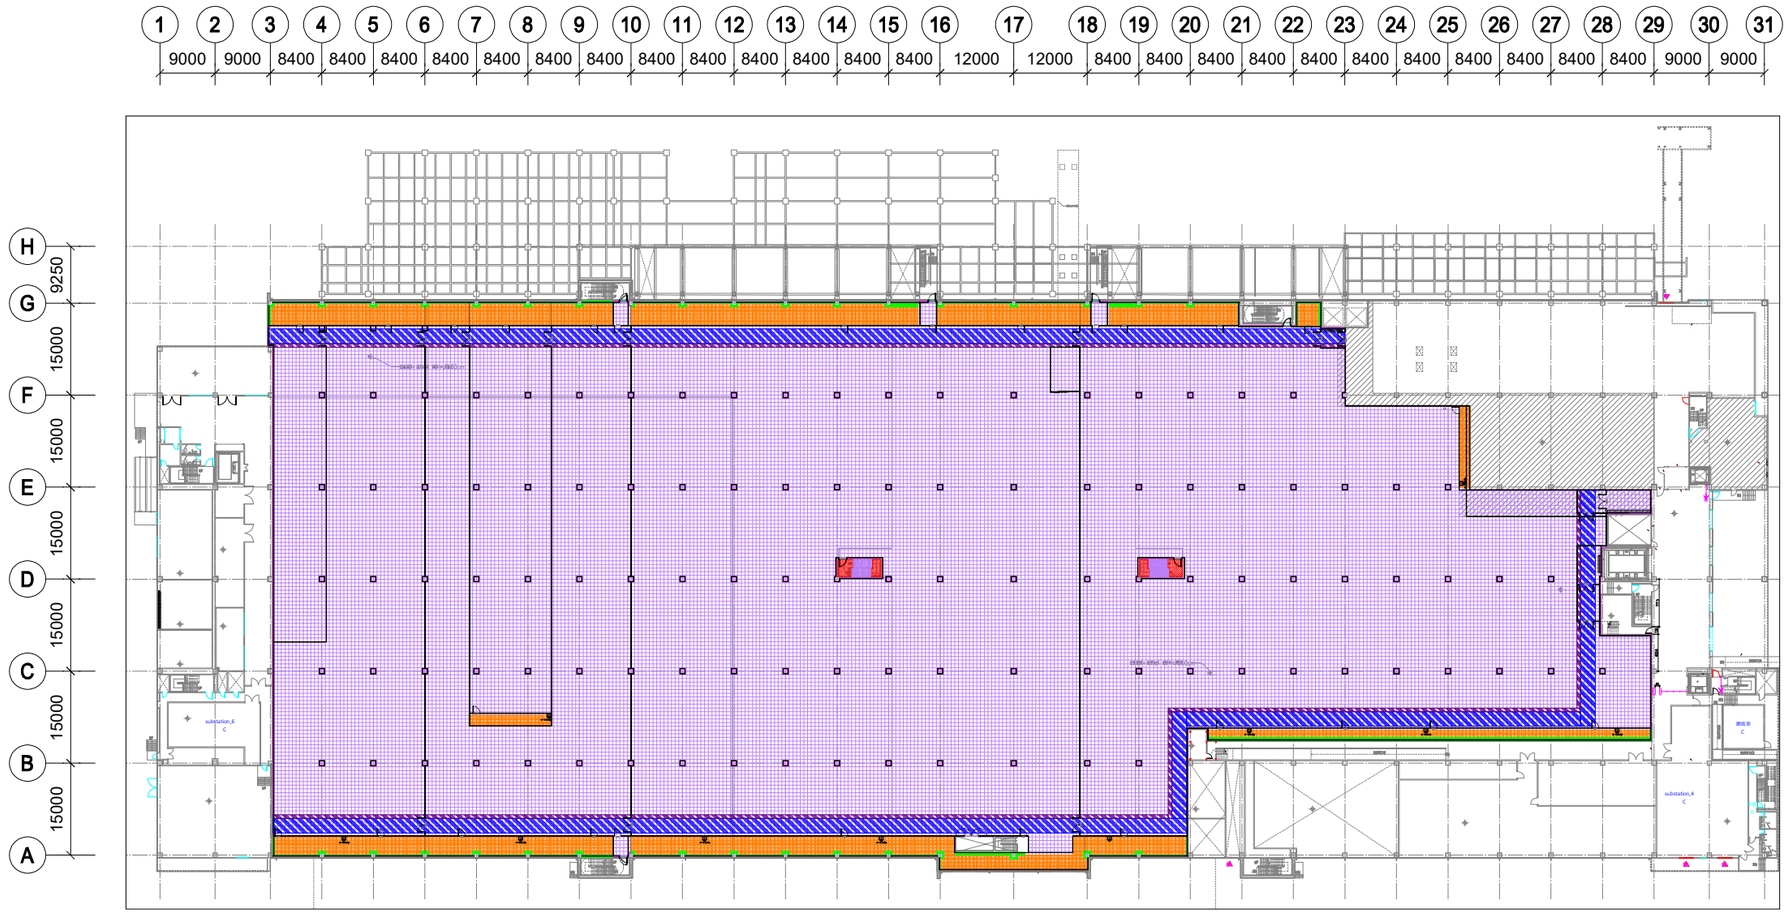


圖 示	說 明
	600×600 高架地板 H=550mm (1500型)
	600×600 高架地板 H=550mm (1500型) 須預降5mm貼白鐵面板,
	600×600 高架地板 H=550mm (1500型) MOVE-IN動線
	600×600 格柵板 H=550mm (1500型)
	600×600 17% 蜂巢板全面積 45%
	RC& 高架地板 SUS收邊板
	潔淨梯鋪止滑PVC地磚- 平台
	潔淨梯鋪止滑PVC地磚- 階梯

OWNER / DEVELOPER

micron

ARCHITECTURAL CONSULTANT

QUO 陳昆豐建築師事務所

CIVIL & STRUCTURAL CONSULTANT

禾森工程顧問有限公司

MECHANICAL & ELECTRICAL CONSULTANT & CONTRACTOR

YKE 洋基工程股份有限公司 YANKEY Engineering Co.,Ltd

SUB-CONTRACTOR

PROJECT ADDRESS

KEY PLAN

REV	DATE	DESCRIPTION	ISSUED BY

Revisions

PROJECT TITLE

美光台南廠188K增建工程

MECH

PROJECT PHASE

Concept Design

DRAWING TITLE

DE_MMTN_F2_B002_B_RAFL_2L10

F2 L10 高架地板平面配置圖

S-Fab L10 RF LAYOUT

DESIGNED : DRAWN : CHECKED :

DATE : 2025/08/17 JOB NO. : SCALE : **A3:1/1000**

DRAWING NO. REV

DE_MMTN_F2_B002_B_RAFL_2L10 **A**

[SHEET PURPOSE] SHEET: SIZE