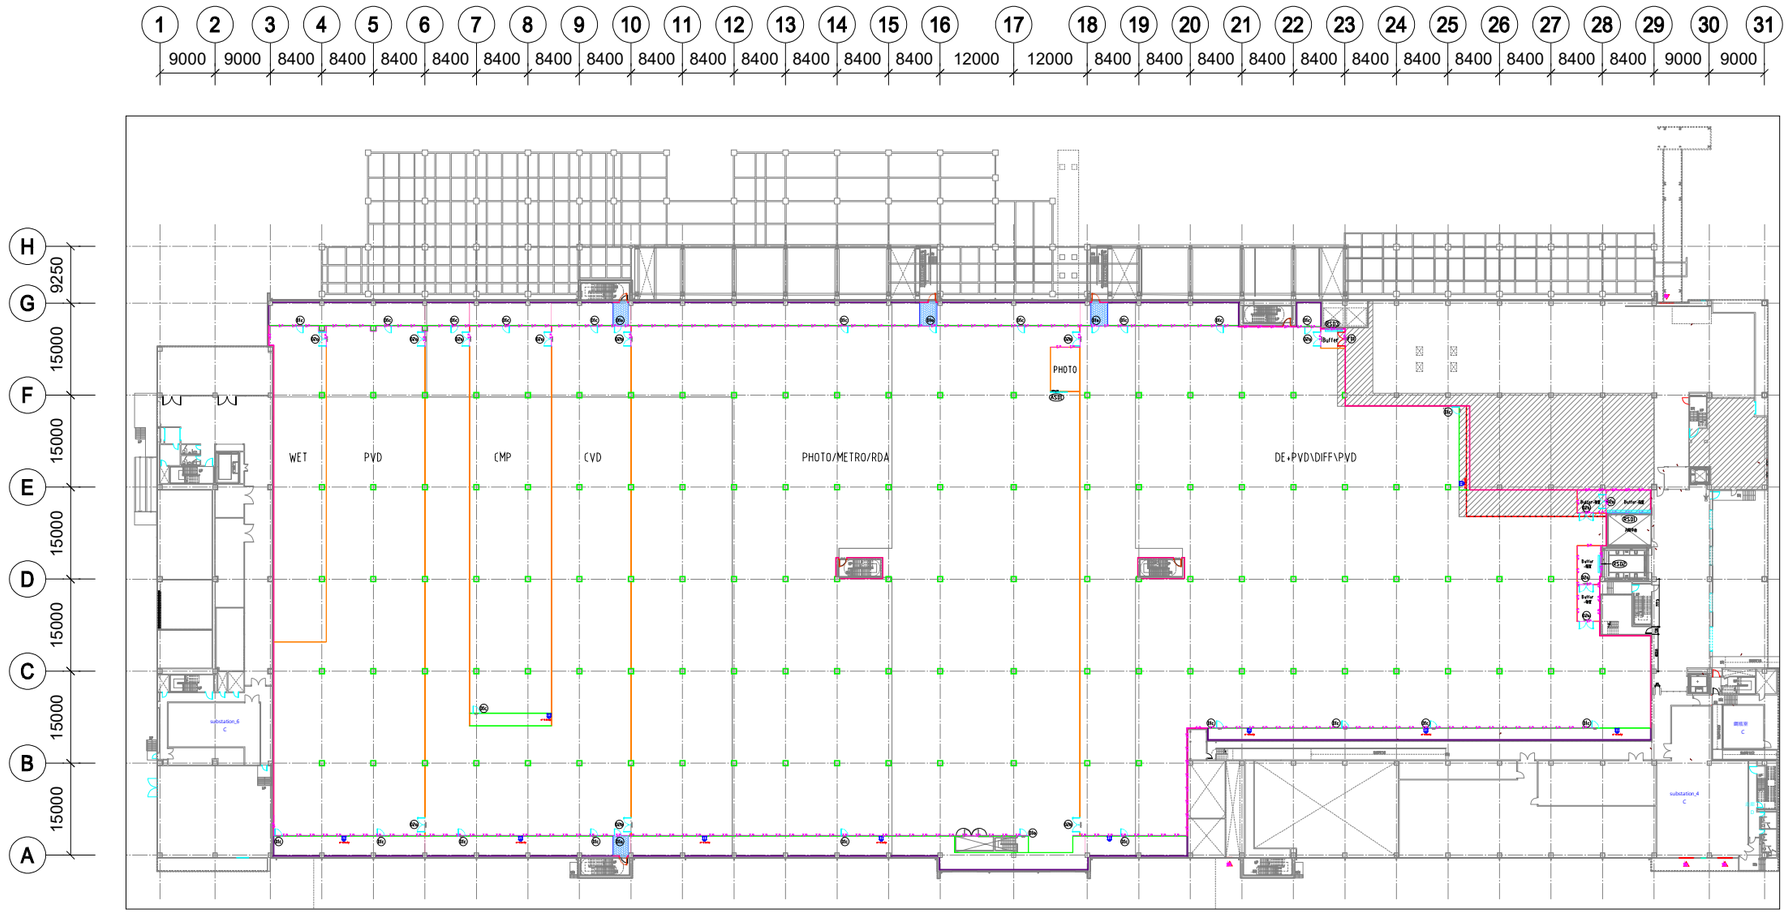

MATERIAL	SYMBOL
鋁鋅鋼庫板隔間(t=50mm) 非抗靜電 H=3500mm	
鋁鋅鋼庫板隔間(t=50mm) 雙面抗靜電 H=4200mm	
鋁鋅鋼庫板隔間(t=50mm) 單面抗靜電 H=4200mm	
鋁鋅鋼庫板隔間(t=50mm) 單面抗靜電 H=3000mm	
防火二小時岩棉庫板隔間(t=100mm) 非抗靜電 H=3500mm	
防火二小時岩棉庫板隔間(t=100mm) 非抗靜電 H=7500mm	
防火二小時岩棉庫板隔間(t=100mm) 單面抗靜電 H=7500mm	
DIVIIDER H=3500mm	
DIVIIDER H=7500mm	
牆面/門扇 (FL+1500mm 防刮鋁白鐵牆面 t=1.0mm)	

註:RF 高架地板完整面起算,
庫板寬度為1200mm.

DOOR SYMBOL & LEGEND		
編號	SYMBOL	DESCRIPTION (含門框尺寸)
D1a		單開庫板門 1200W x 2400H 附視窗(白光)
D1b		單開庫板門 1200W x 2400H 附視窗(黃光)
D1c		單開庫板門 1200W x 2400H 把手型 圓形拉環鎖
D2a		雙開庫板門 2400W x 2400H 附視窗(白光)
D2b		雙開庫板門 2400W x 2400H 附視窗(黃光)
D3a		雙開庫板門 2000W x 1700H 附視窗(白光)
D3b		雙開庫板門 2000W x 1700H 附視窗(黃光)
D4		單開鋼板門 900W x 1700H 風門連 (鐵皮上開門,須氣密)
FD1		二小時雙開防火門 2400W x 2400H
FD2		二小時雙開防火門 2000W x 1700H
ASD1		單開自動門 1200W x 2400H 附視窗(白光)
SSD1		二小時鐵捲門 7000W x 3000H (馬達須防爆)
SSD2		二小時鐵捲門 2800W x 3000H (馬達須防爆)
SSD3		二小時鐵捲門 2400W x 3000H (馬達須防爆)
SSD4		二小時鐵捲門 7000W x 1700H (馬達須防爆)
SSD5		二小時鐵捲門 2800W x 1700H (馬達須防爆)
SSD6		二小時鐵捲門 2400W x 1700H (馬達須防爆)

EQUIPMENT SYMBOL & LEGEND		
SYMBOL	DESCRIPTION 單位:mm	REMARKS
	爬梯(STAINLESS STEEL)	LAD

OWNER / DEVELOPER
micron

ARCHITECTURAL CONSULTANT
QUO 陳昆豐建築師事務所

CIVIL & STRUCTURAL CONSULTANT
禾森工程顧問有限公司

MECHANICAL & ELECTRICAL CONSULTANT & CONTRACTOR
YKE 洋基工程股份有限公司 YANKEY Engineering Co.,Ltd

SUB-CONTRACTOR

PROJECT ADDRESS

KEY PLAN

REV	DATE	DESCRIPTION	ISSUED BY

Revisions

PROJECT TITLE
美光台南廠188K增建工程
MECH

PROJECT PHASE
Concept Design

DRAWING TITLE
DE_MMTN_F2_B002_D_PRTN_2L10
F2 L10 隔間平面配置圖
S-Fab L10 PA LAYOUT

DESIGNED : DRAWN : CHECKED :
DATE : 2025/08/17 JOB NO. : SCALE : A3:1/1000
DRAWING NO. REV
DE_MMTN_F2_B002_D_PRTN_2L10 A
SHEET: SIZE
[SHEET PURPOSE]