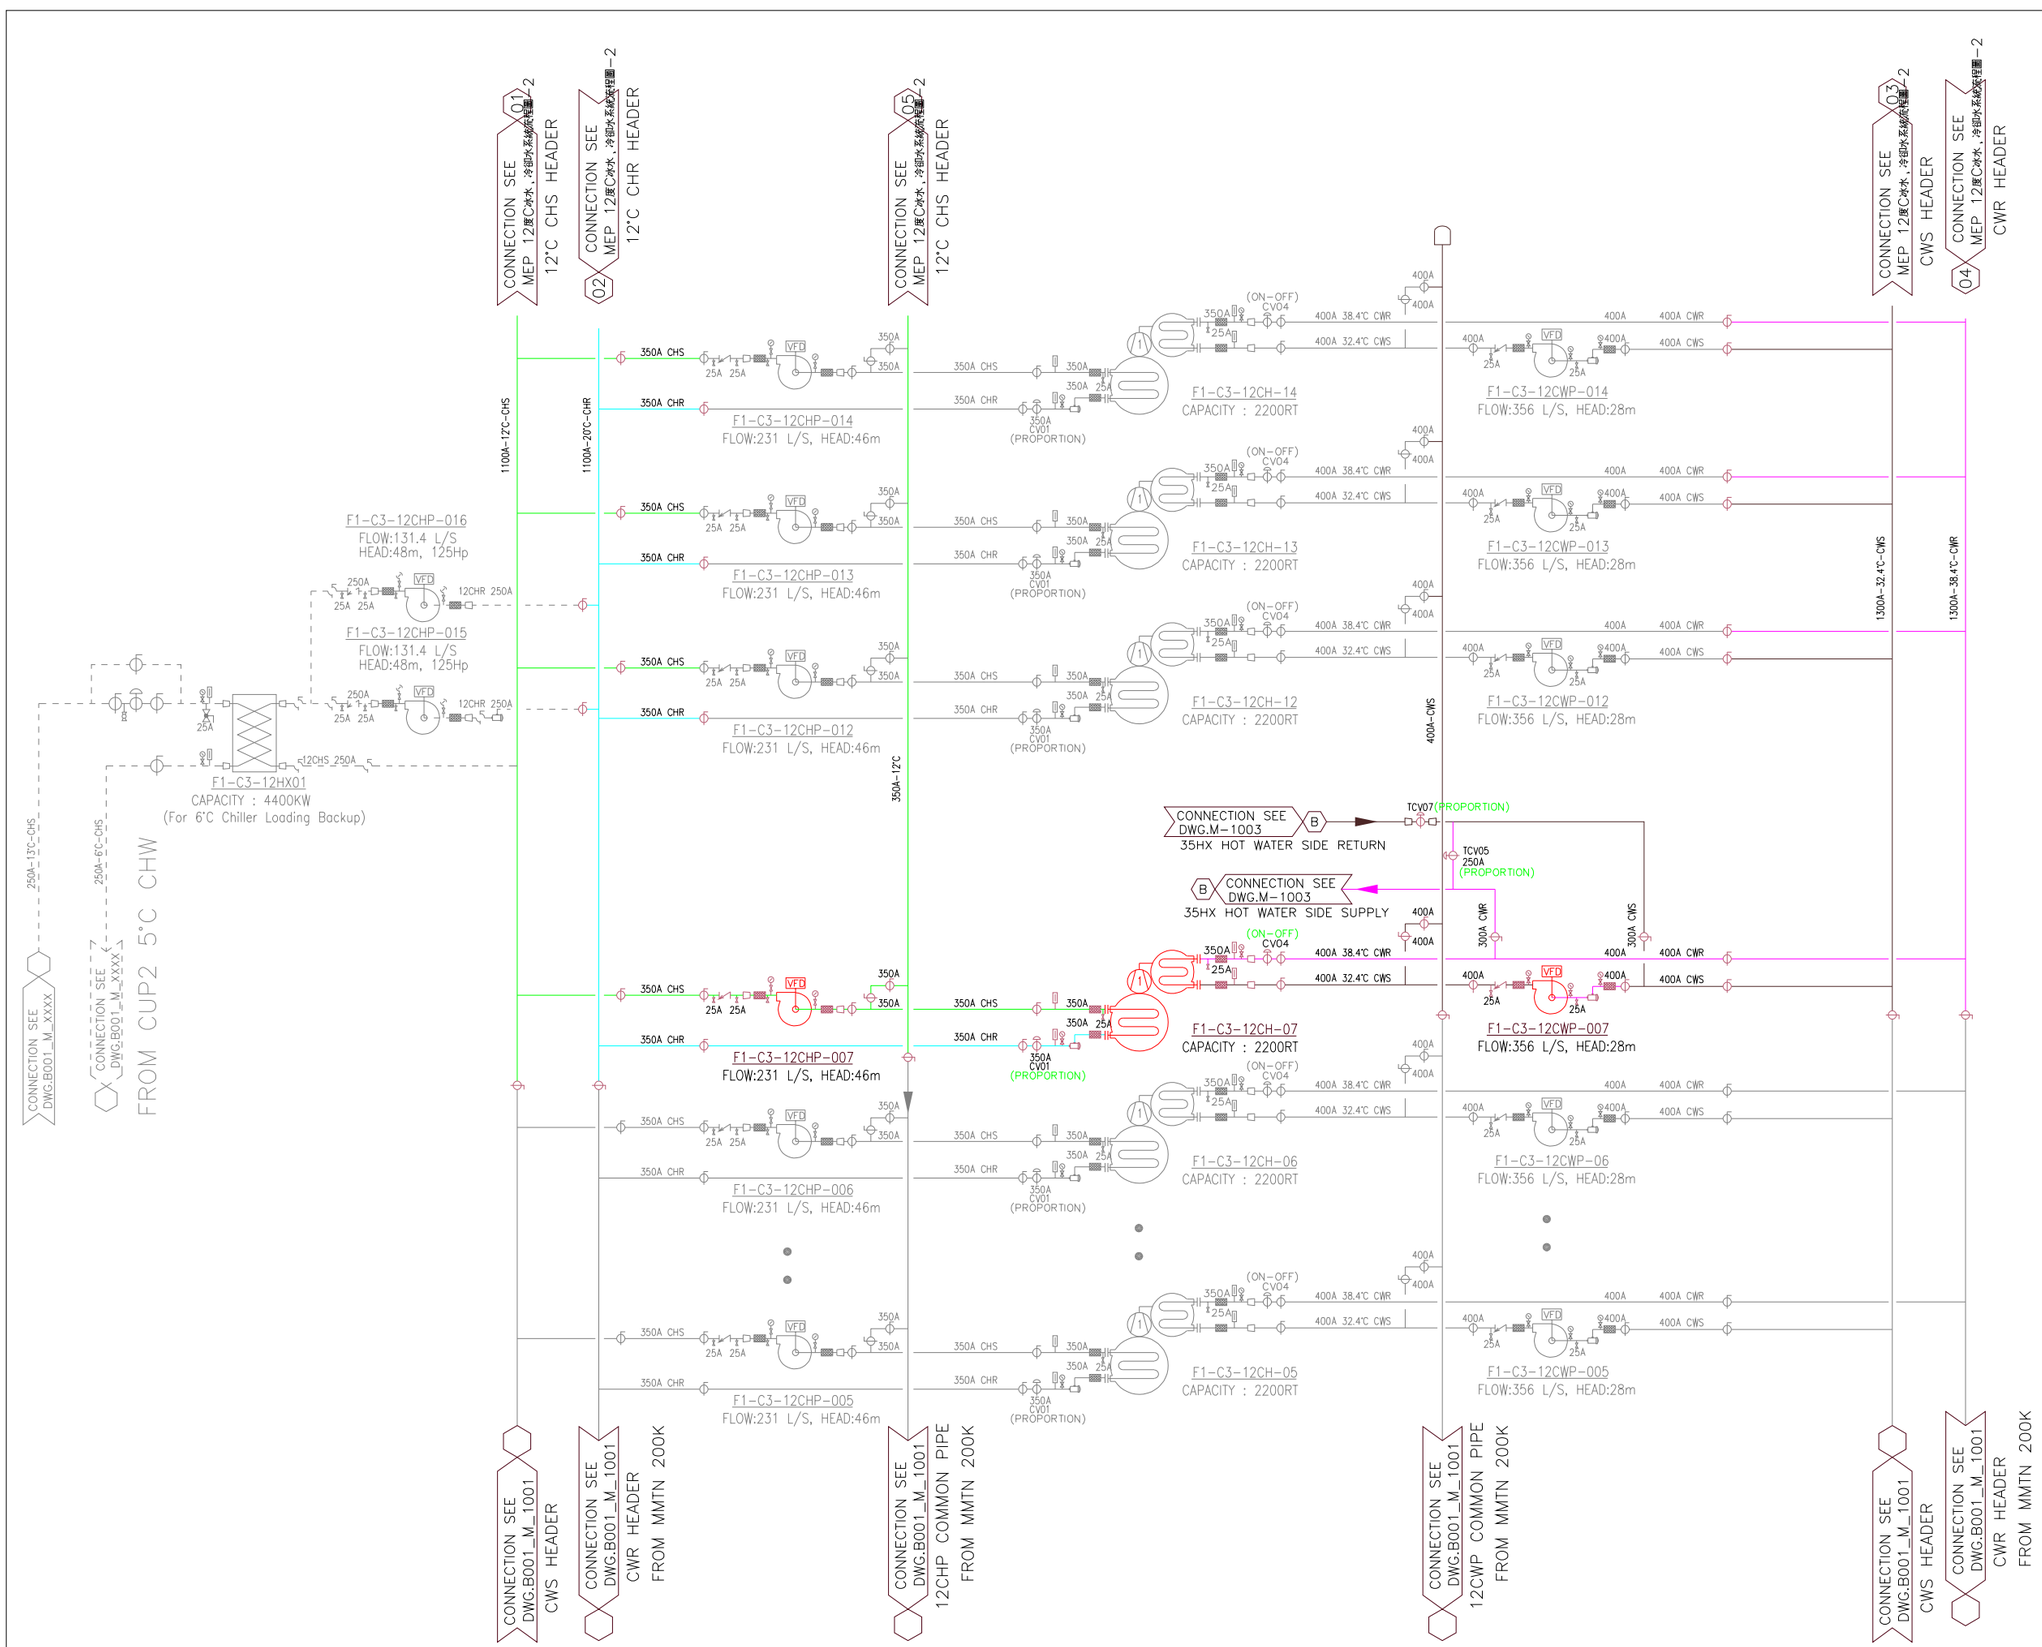

OWNER / DEVELOPER

micron

ARCHITECTURAL CONSULTANT

QUO 陳昆豐建築師事務所

CIVIL & STRUCTURAL CONSULTANT

禾森工程顧問有限公司

MECHANICAL & ELECTRICAL CONSULTANT & CONTRACTOR

洋基工程股份有限公司
YANKEY Engineering Co.,Ltd

SUB-CONTRACTOR

PROJECT ADDRESS

KEY PLAN

REV	DATE	DESCRIPTION	ISSUED BY
		Revisions	

PROJECT TITLE

美光台南廠188K增建工程
MECH

PROJECT PHASE

Concept Design

DRAWING TITLE

DE_MMTN_F2_B002_M_CHWT_1001
MEP 12度C冰水、冷卻水系統流程圖-1
FLOW DIAGRAM-12°C/20°C CHILLED & CONDENSER WATER SYSTEM(1)

DESIGNED :	DRAWN :	CHECKED :
DATE : 2025/08/12	JOB NO. :	SCALE :

DRAWING NO. **DE_MMTN_F2_B002_M_CHWT_1001** REV **A**

[SHEET PURPOSE] SHEET: SIZE