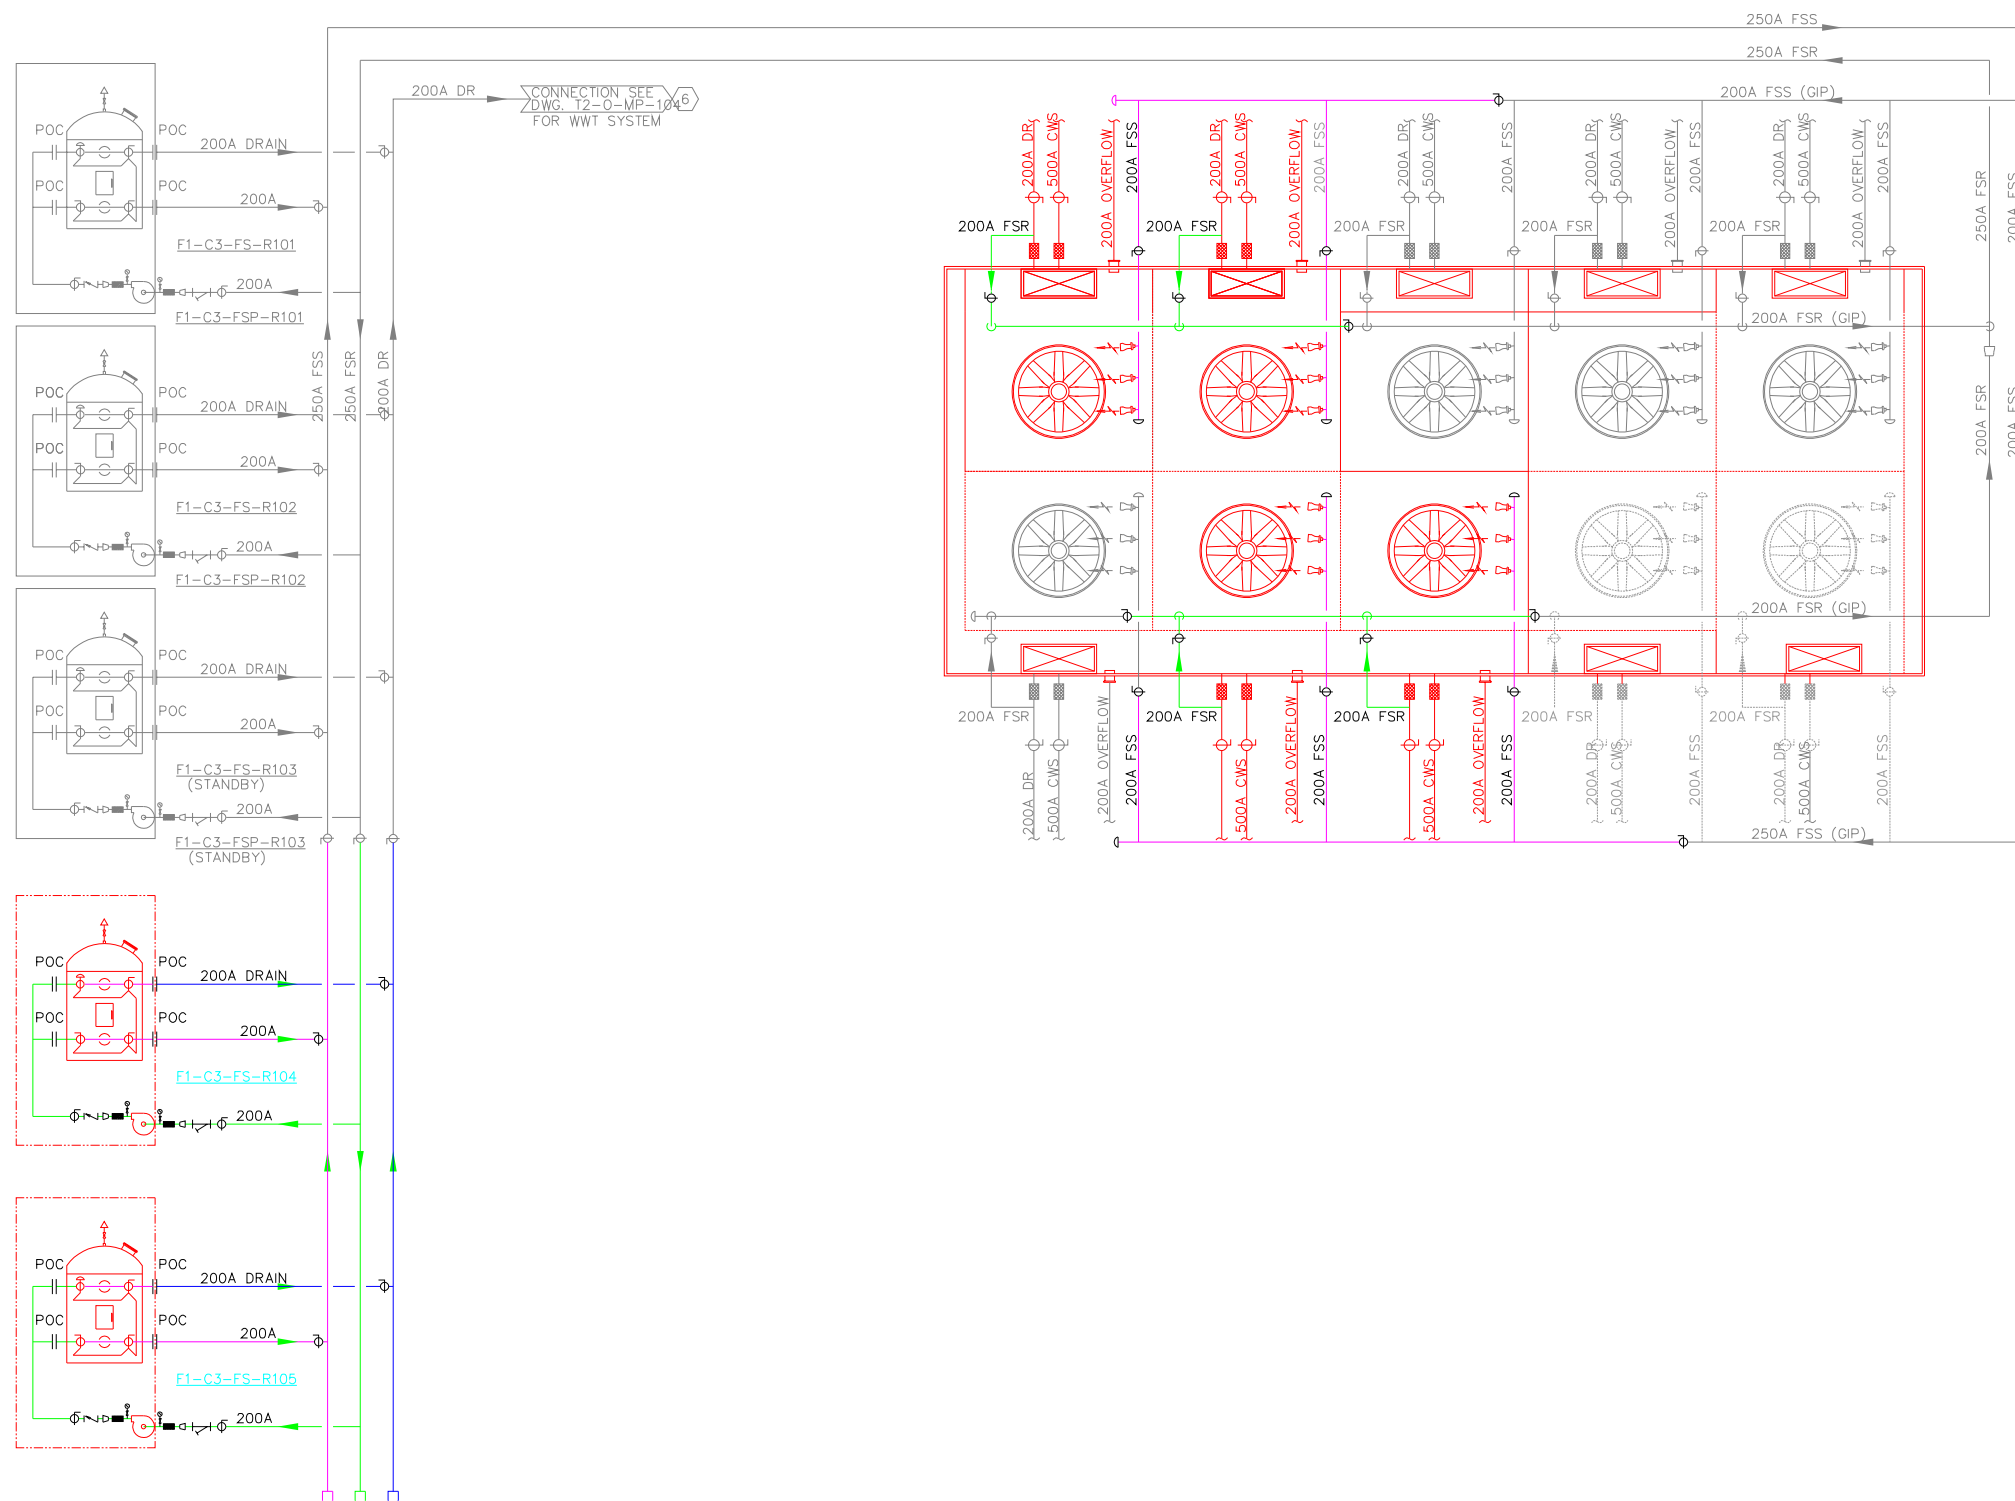


[illegible]

PROJECT TITLE
美光台南廠188K增建工程

PROJECT PHASE	Concept Design
---------------	----------------

DRAWING TITLE

DE_MMTN_F2_B002_M_CHWT_1006

MEP冷卻水塔沙濾系統流程圖

FLOW DIAGRAM-COOLING TOWER

FILTRATION SYSTEM

DESIGNED :	DRAWN :	CHECKED :
DATE : 2025/08/06	JOB NO :	SCALE :

DRAWING NO. **DE_MMTN_F2_B002_M_CHWT_1006**

[SHEET PURPOSE] SHEET: SIZE: