


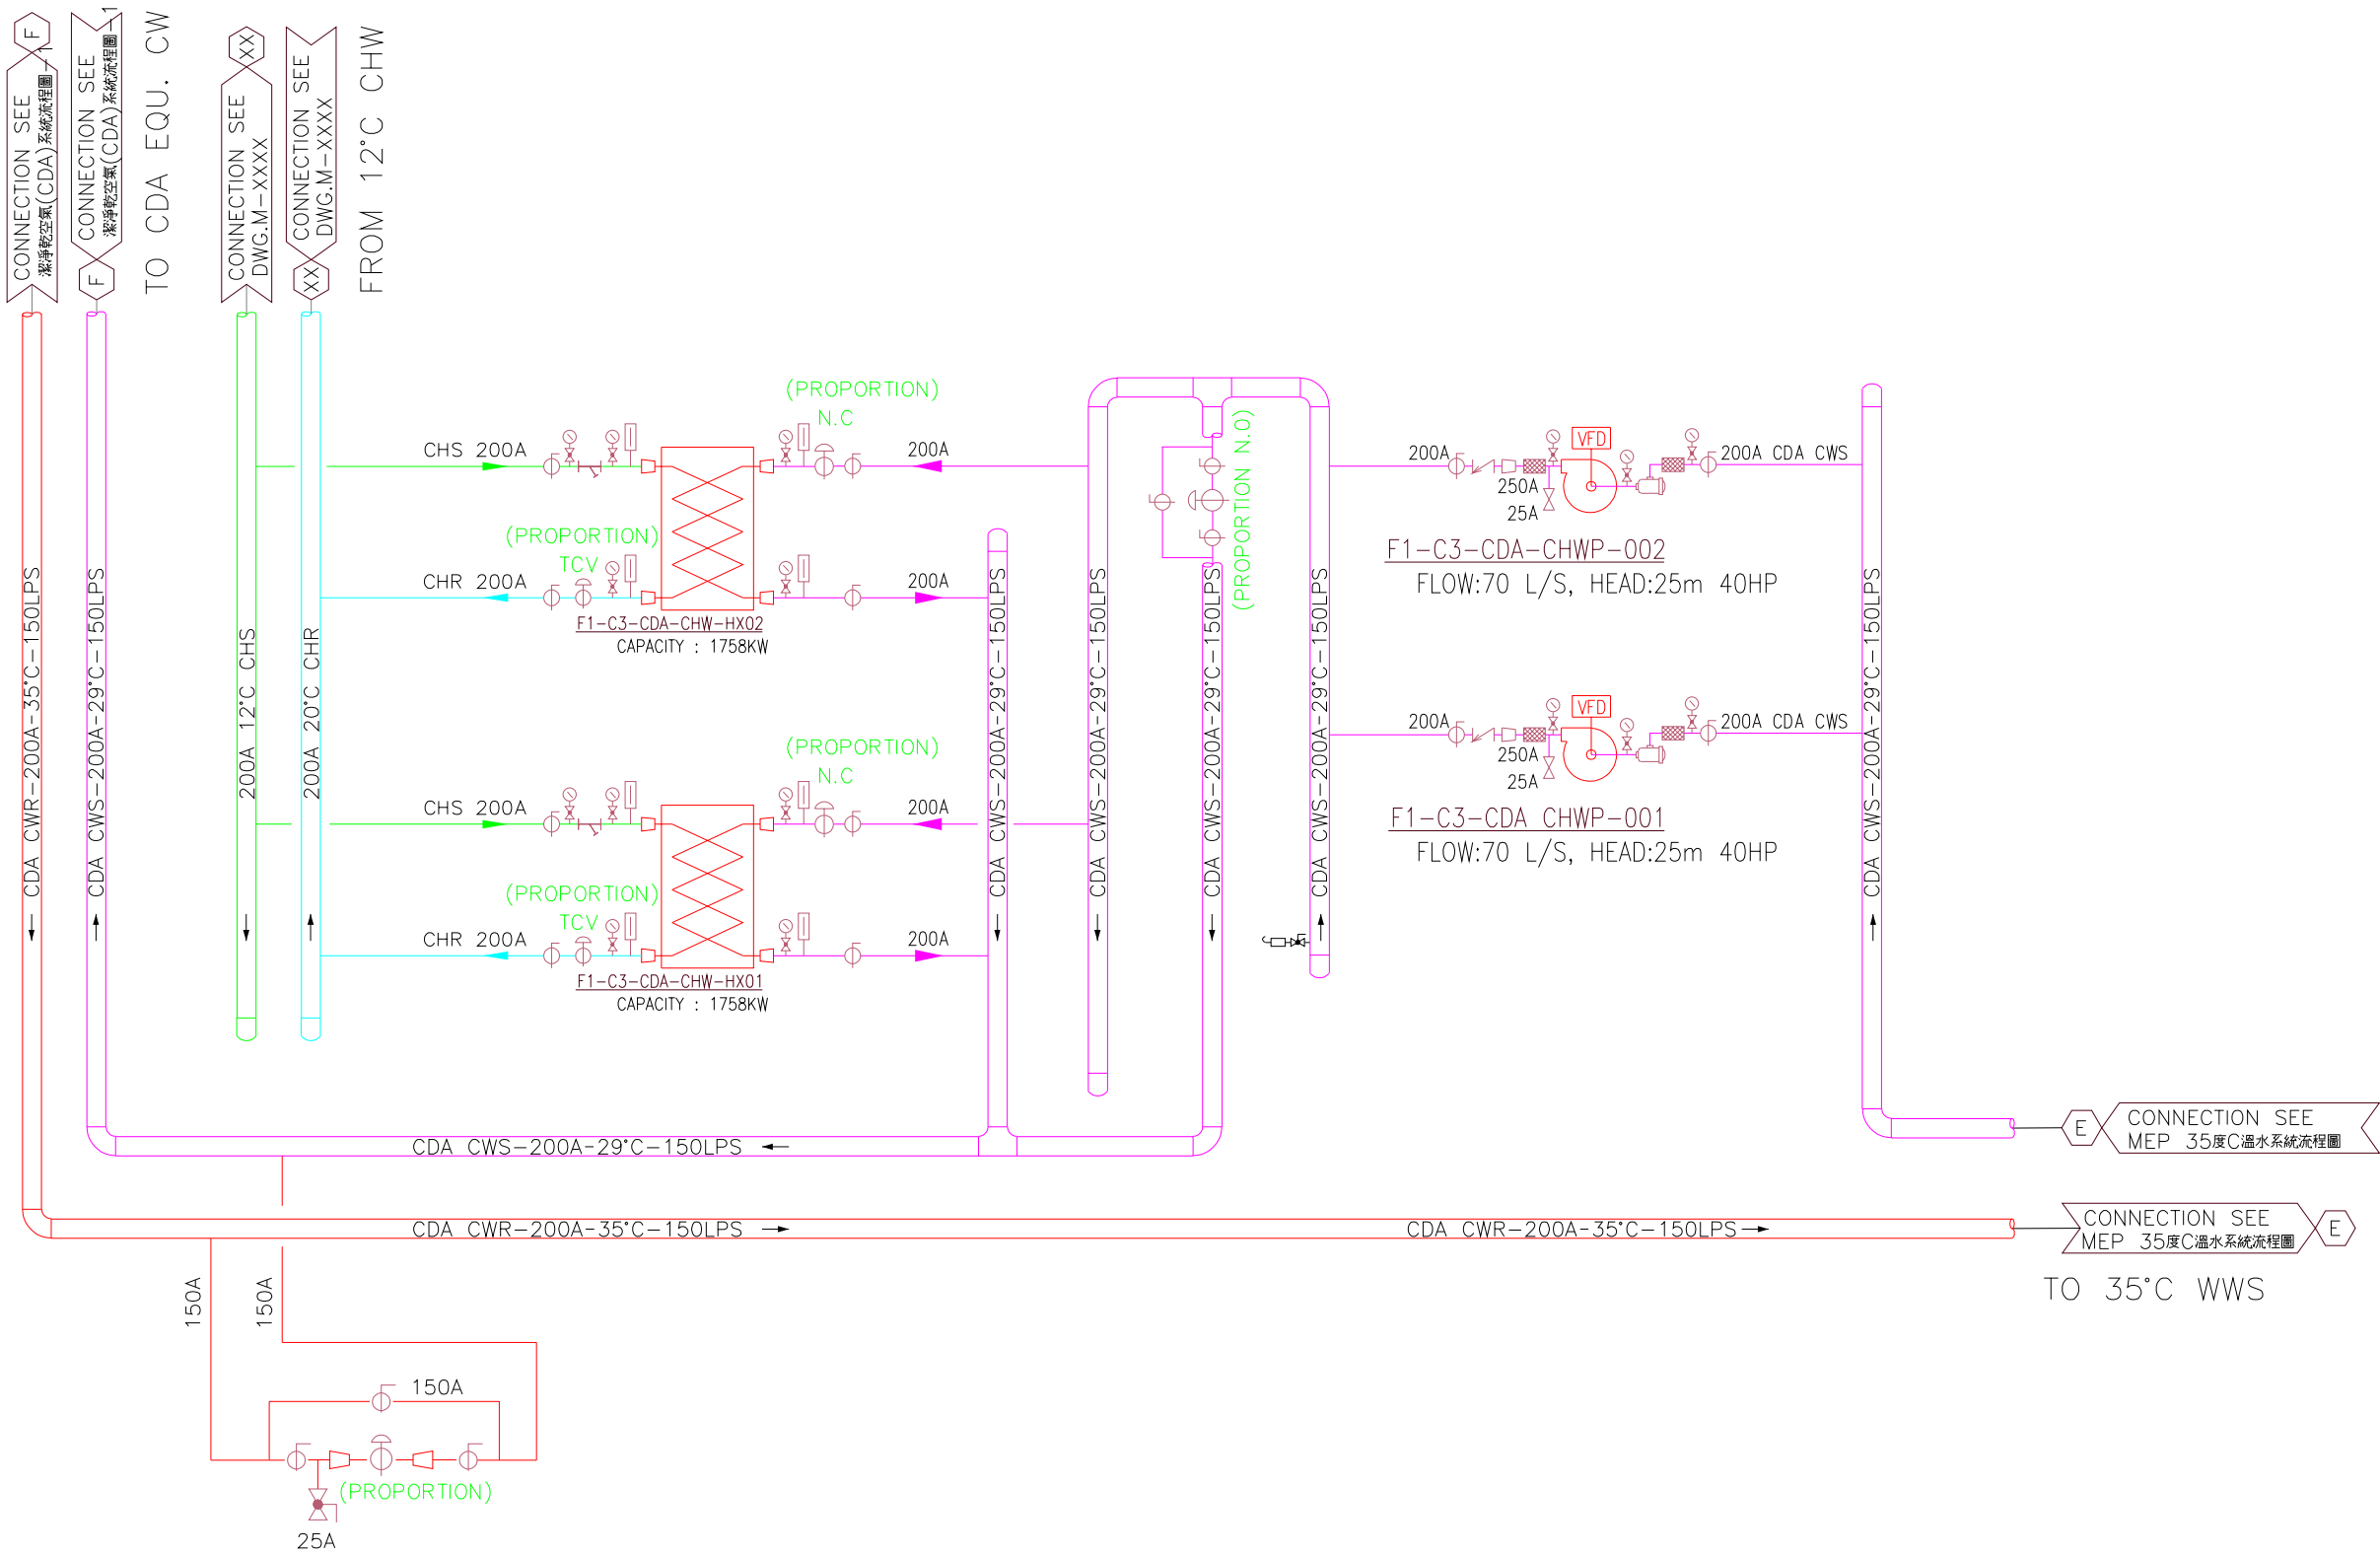

REV	DATE	DESCRIPTION Revisions	ISSUED BY

PROJECT TITLE
美光台南廠188K增建工程

PROJECT PHASE
MECH
Concept Design

DRAWING TITLE
DE_MMTN_F2_B002_M_CHWT_1007
MEP CDA熱回收系統流程圖
**FLOW DIAGRAM-
CDA COOLING WATER SYSTEM**

DESIGNED : DRAWN : CHECKED :
DATE : 2025/08/12 JOB NO. : SCALE :

DRAWING NO. REV
DE_MMTN_F2_B002_M_CHWT_1007 A

[SHEET PURPOSE] SHEET: SIZE