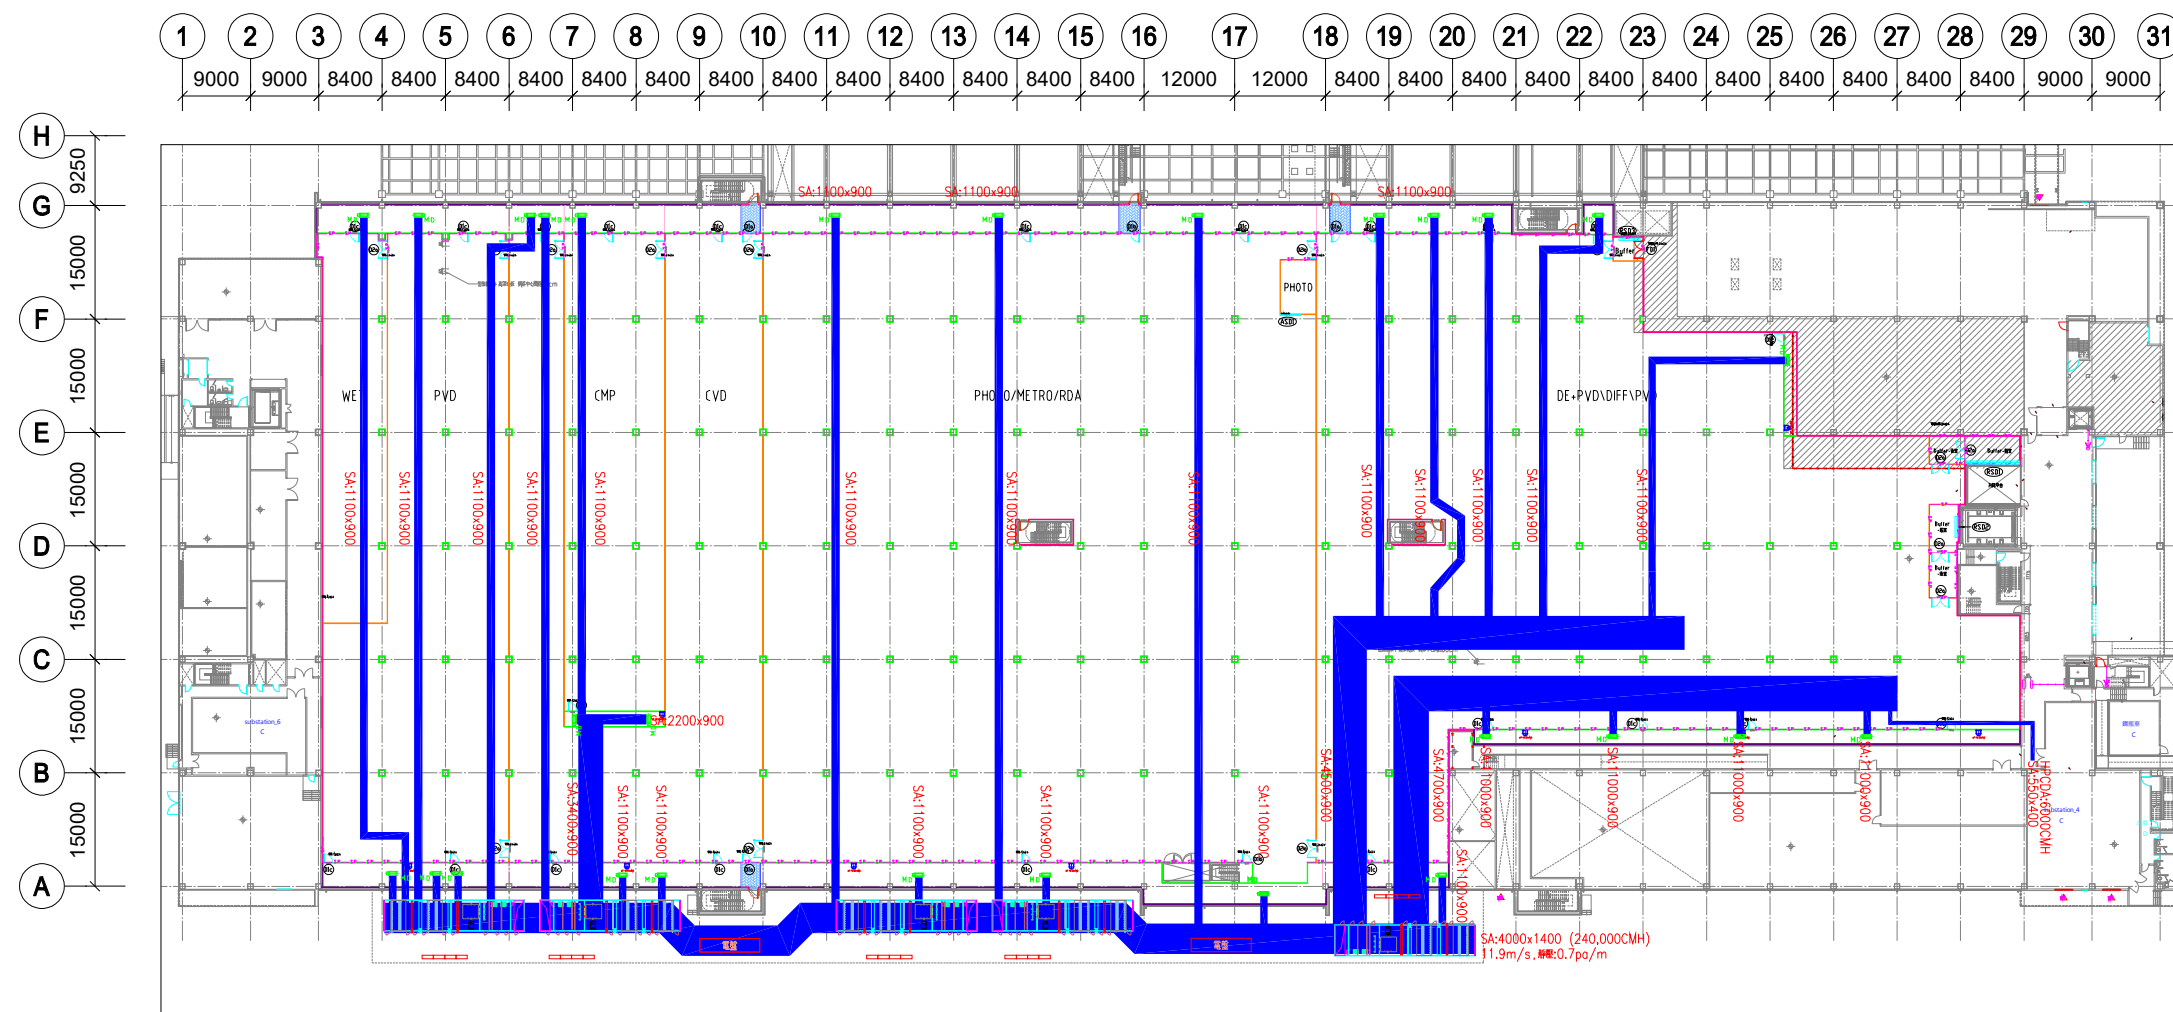


[illegible]

PROJECT TITLE			
美光台南廠188K增建工程			
MECH			
PROJECT PHASE			
Concept Design			
DRAWING TITLE			
DE_MMTN_F2_B002_M_DUCT_2L15			
F2 L15 空調風管平面配置圖			
F2 L15 MECHICAL DUCT LAYOUT			
DESIGNED : _____			
DRAWN : _____		CHECKED : _____	
DATE : 2025/08/17	JOB NO. : _____	SCALE : A3:1/1000	
DRAWING NO.			REV
DE_MMTN_F2_B002_M_DUCT_2L15			A
[SHEET PURPOSE]			SHEET
			SIZE