


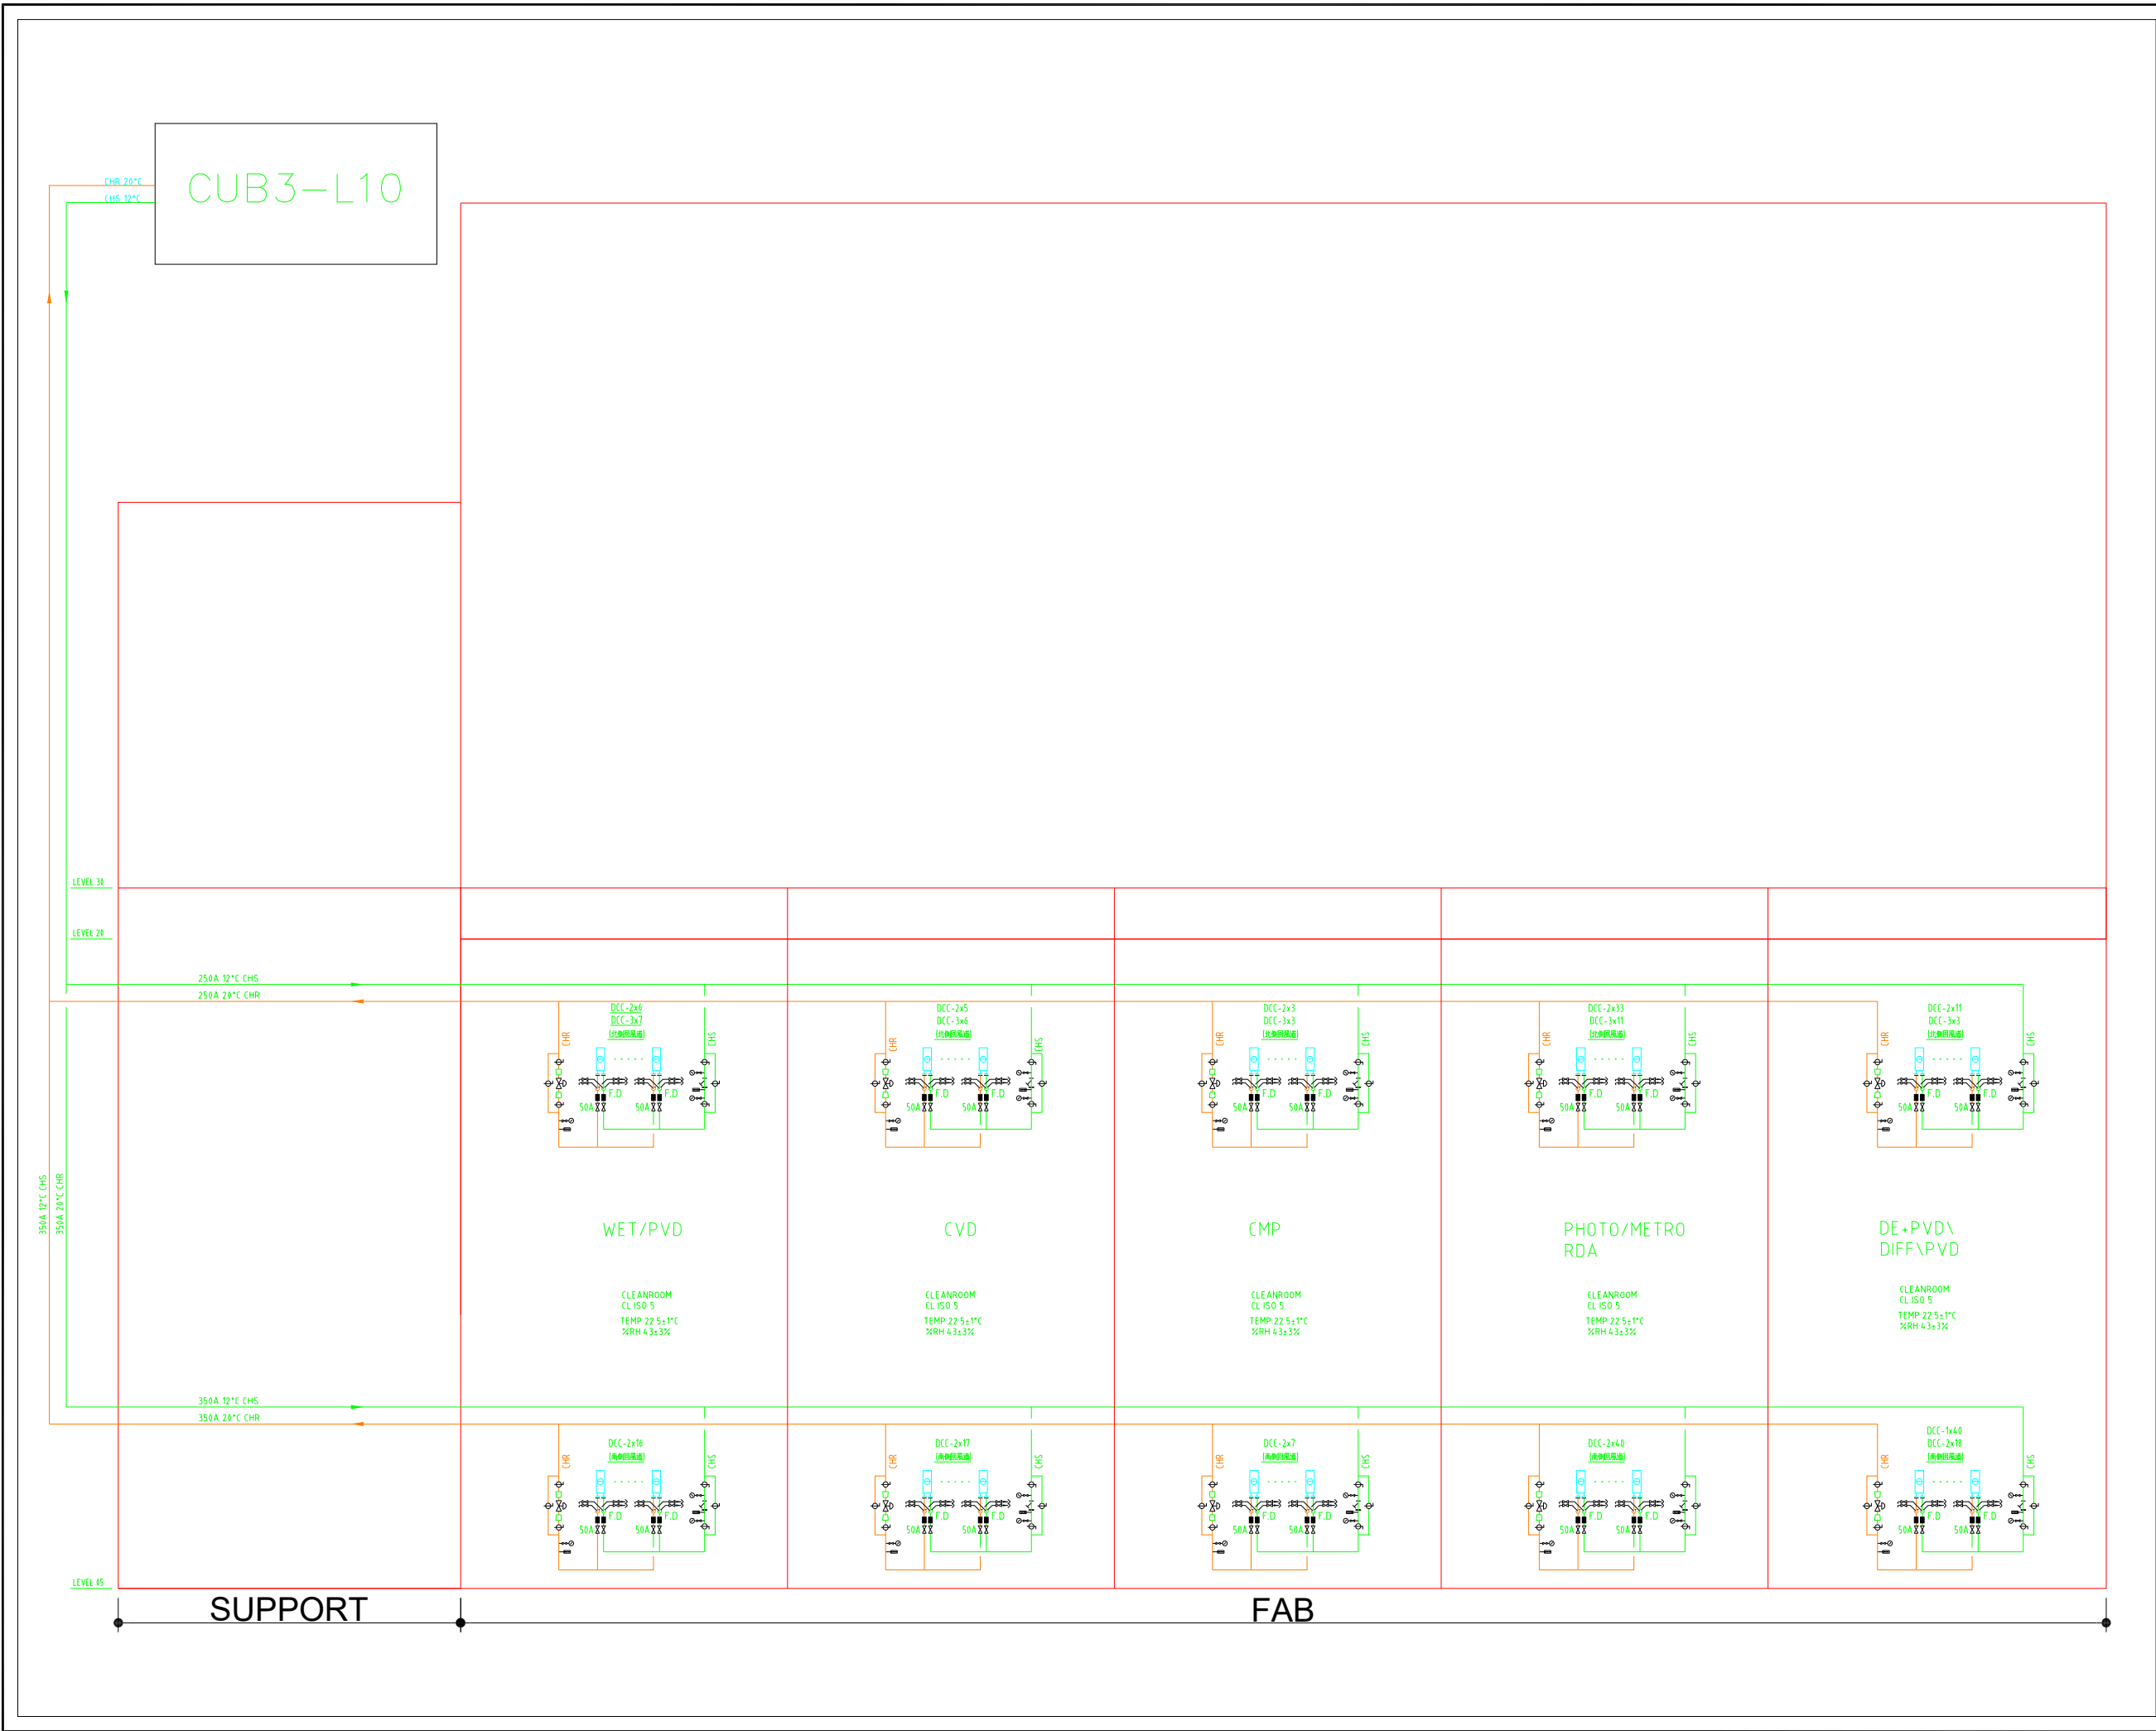

OWNER / DEVELOPER

ARCHITECTURAL CONSULTANT

陳昆豐建築師事務所

CIVIL & STRUCTURAL CONSULTANT

禾森工程顧問有限公司

MECHANICAL & ELECTRICAL CONSULTANT & CONTRACTOR

洋基工程股份有限公司
YANKEY Engineering Co.,Ltd

SUB-CONTRACTOR

PROJECT ADDRESS

KEY PLAN

REV	DATE	DESCRIPTION Revisions	ISSUED BY

PROJECT TITLE

美光台南廠188K增建工程

MECH

PROJECT PHASE

Concept Design

DRAWING TITLE

DE_MMTN_F2_B002_M_PIPE_1001
CR DCC水管系統流程圖
FLOW DIAGRAM-DCC PIPE SYSTEM

DESIGNED :

DRAWN :

CHECKED :

DATE : 2025/08/14

JOB NO. :

SCALE :

DRAWING NO.

DE_MMTN_F2_B002_M_PIPE_1001

REV

A

[SHEET PURPOSE]

SHEET:

SIZE