

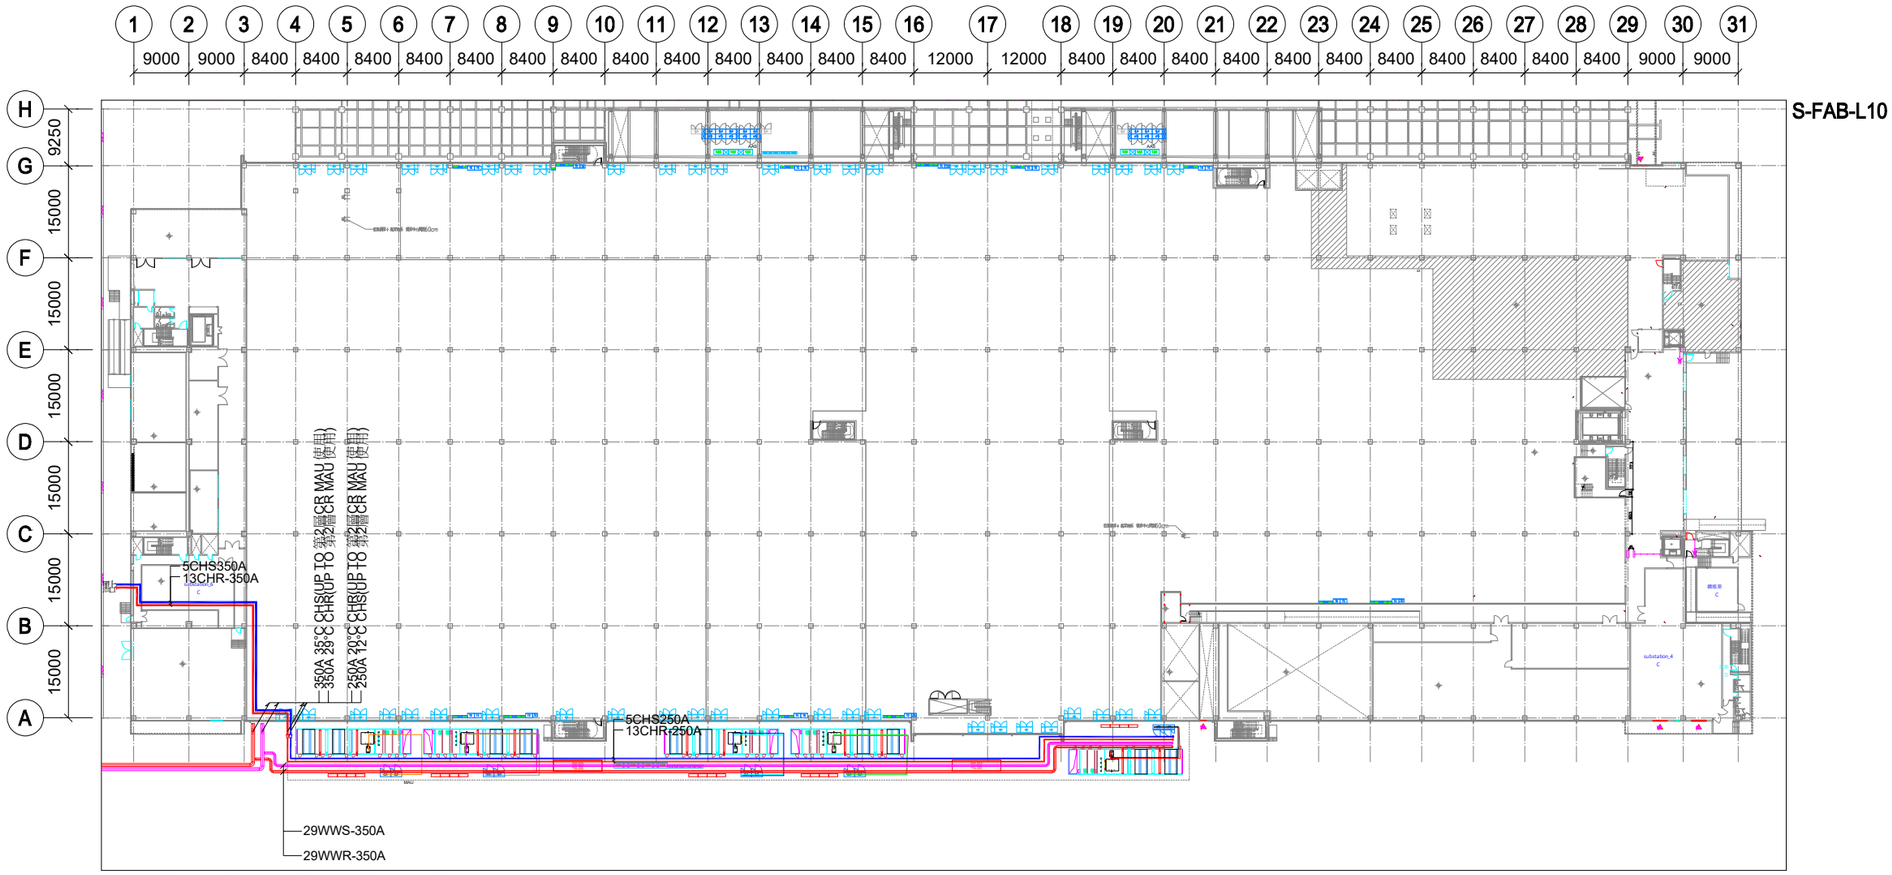


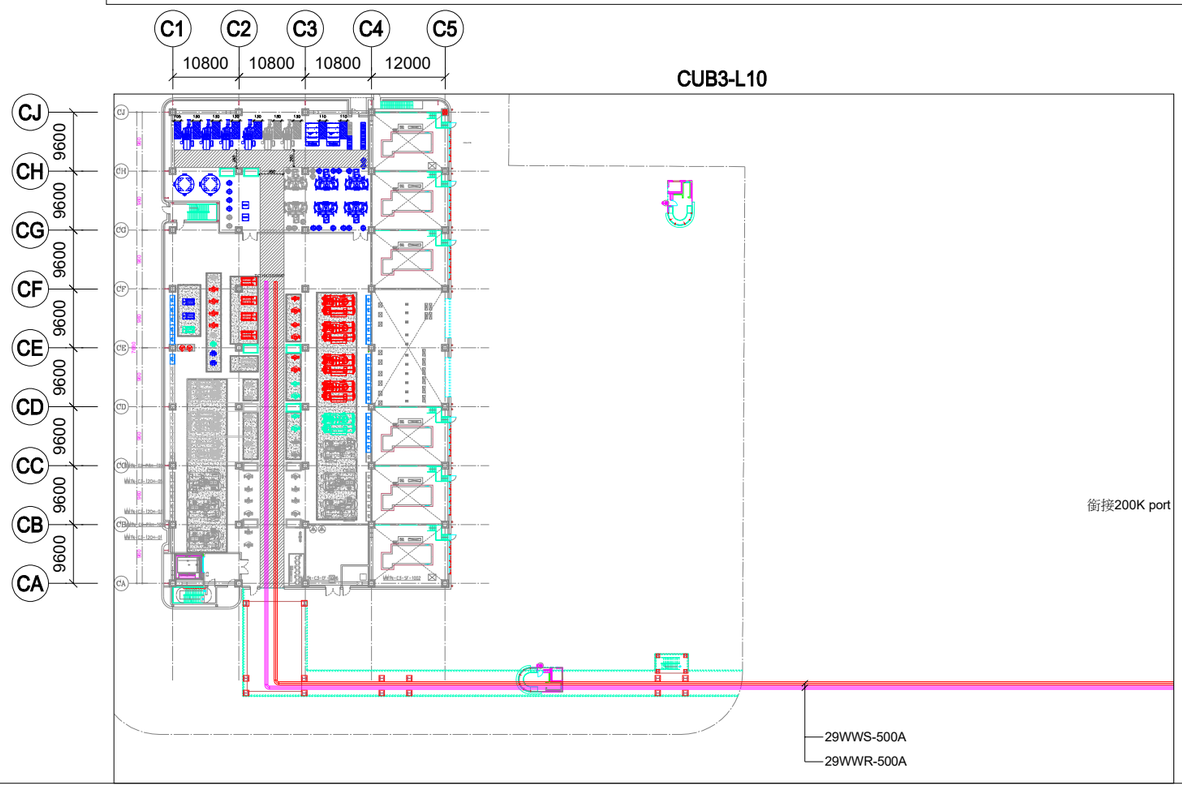

管橋剖面位置

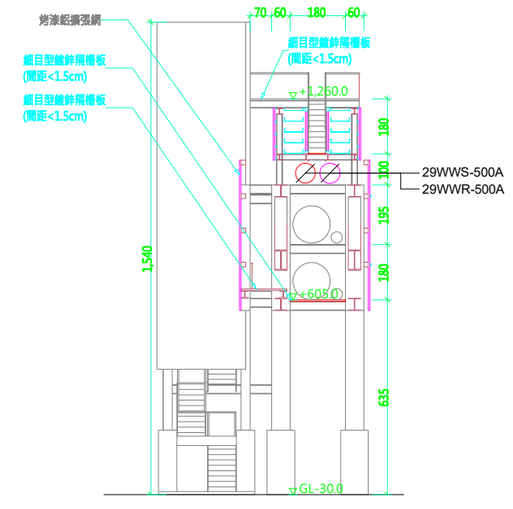

OWNER / DEVELOPER

micron

ARCHITECTURAL CONSULTANT

QUO 陳昆豐建築師事務所

CIVIL & STRUCTURAL CONSULTANT

森 禾森工程顧問有限公司

MECHANICAL & ELECTRICAL CONSULTANT & CONTRACTOR

YKE 洋基工程股份有限公司 YANKEY Engineering Co.,Ltd

SUB-CONTRACTOR

PROJECT ADDRESS

KEY PLAN

REV	DATE	DESCRIPTION	ISSUED BY

Revisions

PROJECT TITLE

美光台南廠188K增建工程

MECH

PROJECT PHASE

Concept Design

DRAWING TITLE

DE_MMTN_F2_B002_M_WARM_2L10

F2 L10 35度C 溫水管路平面圖

F2 L10 35℃ WARM WATER PIPE LAYOUT

DESIGNED : DRAWN : CHECKED :

DATE : 2025/08/17 JOB NO. : SCALE : A3:1/1000

DRAWING NO. REV

DE_MMTN_F2_B002_M_WARM_2L10 A

SHEET: SIZE

[SHEET PURPOSE]