


CONFIDENTIAL NOTICE: THE CONTENT OF THIS DOCUMENT IS SENSITIVE INFORMATION AND IS PROTECTED BY COPYRIGHT LAWS AND RELEVANT LAWS/REGULATIONS. ONLY EMPLOYEES OF MICRON ARE ALLOWED TO ACCESS AND USE THIS SENSITIVE INFORMATION WITHIN THE WORK SCOPE. UNLESS THERE SPECIFIC AND RESPECTIVE RULES AND REGULATIONS REQUIRED BY AGREEMENT WHICH IS NOT ALLOWED TO COPY, REPRODUCE, DISTRIBUTE PUBLICLY OR OTHERWISE IN WHOLE OR IN PART TO ANY OTHER PARTY WITHOUT CTCI'S PRIOR AND WRITTEN CONSENT.

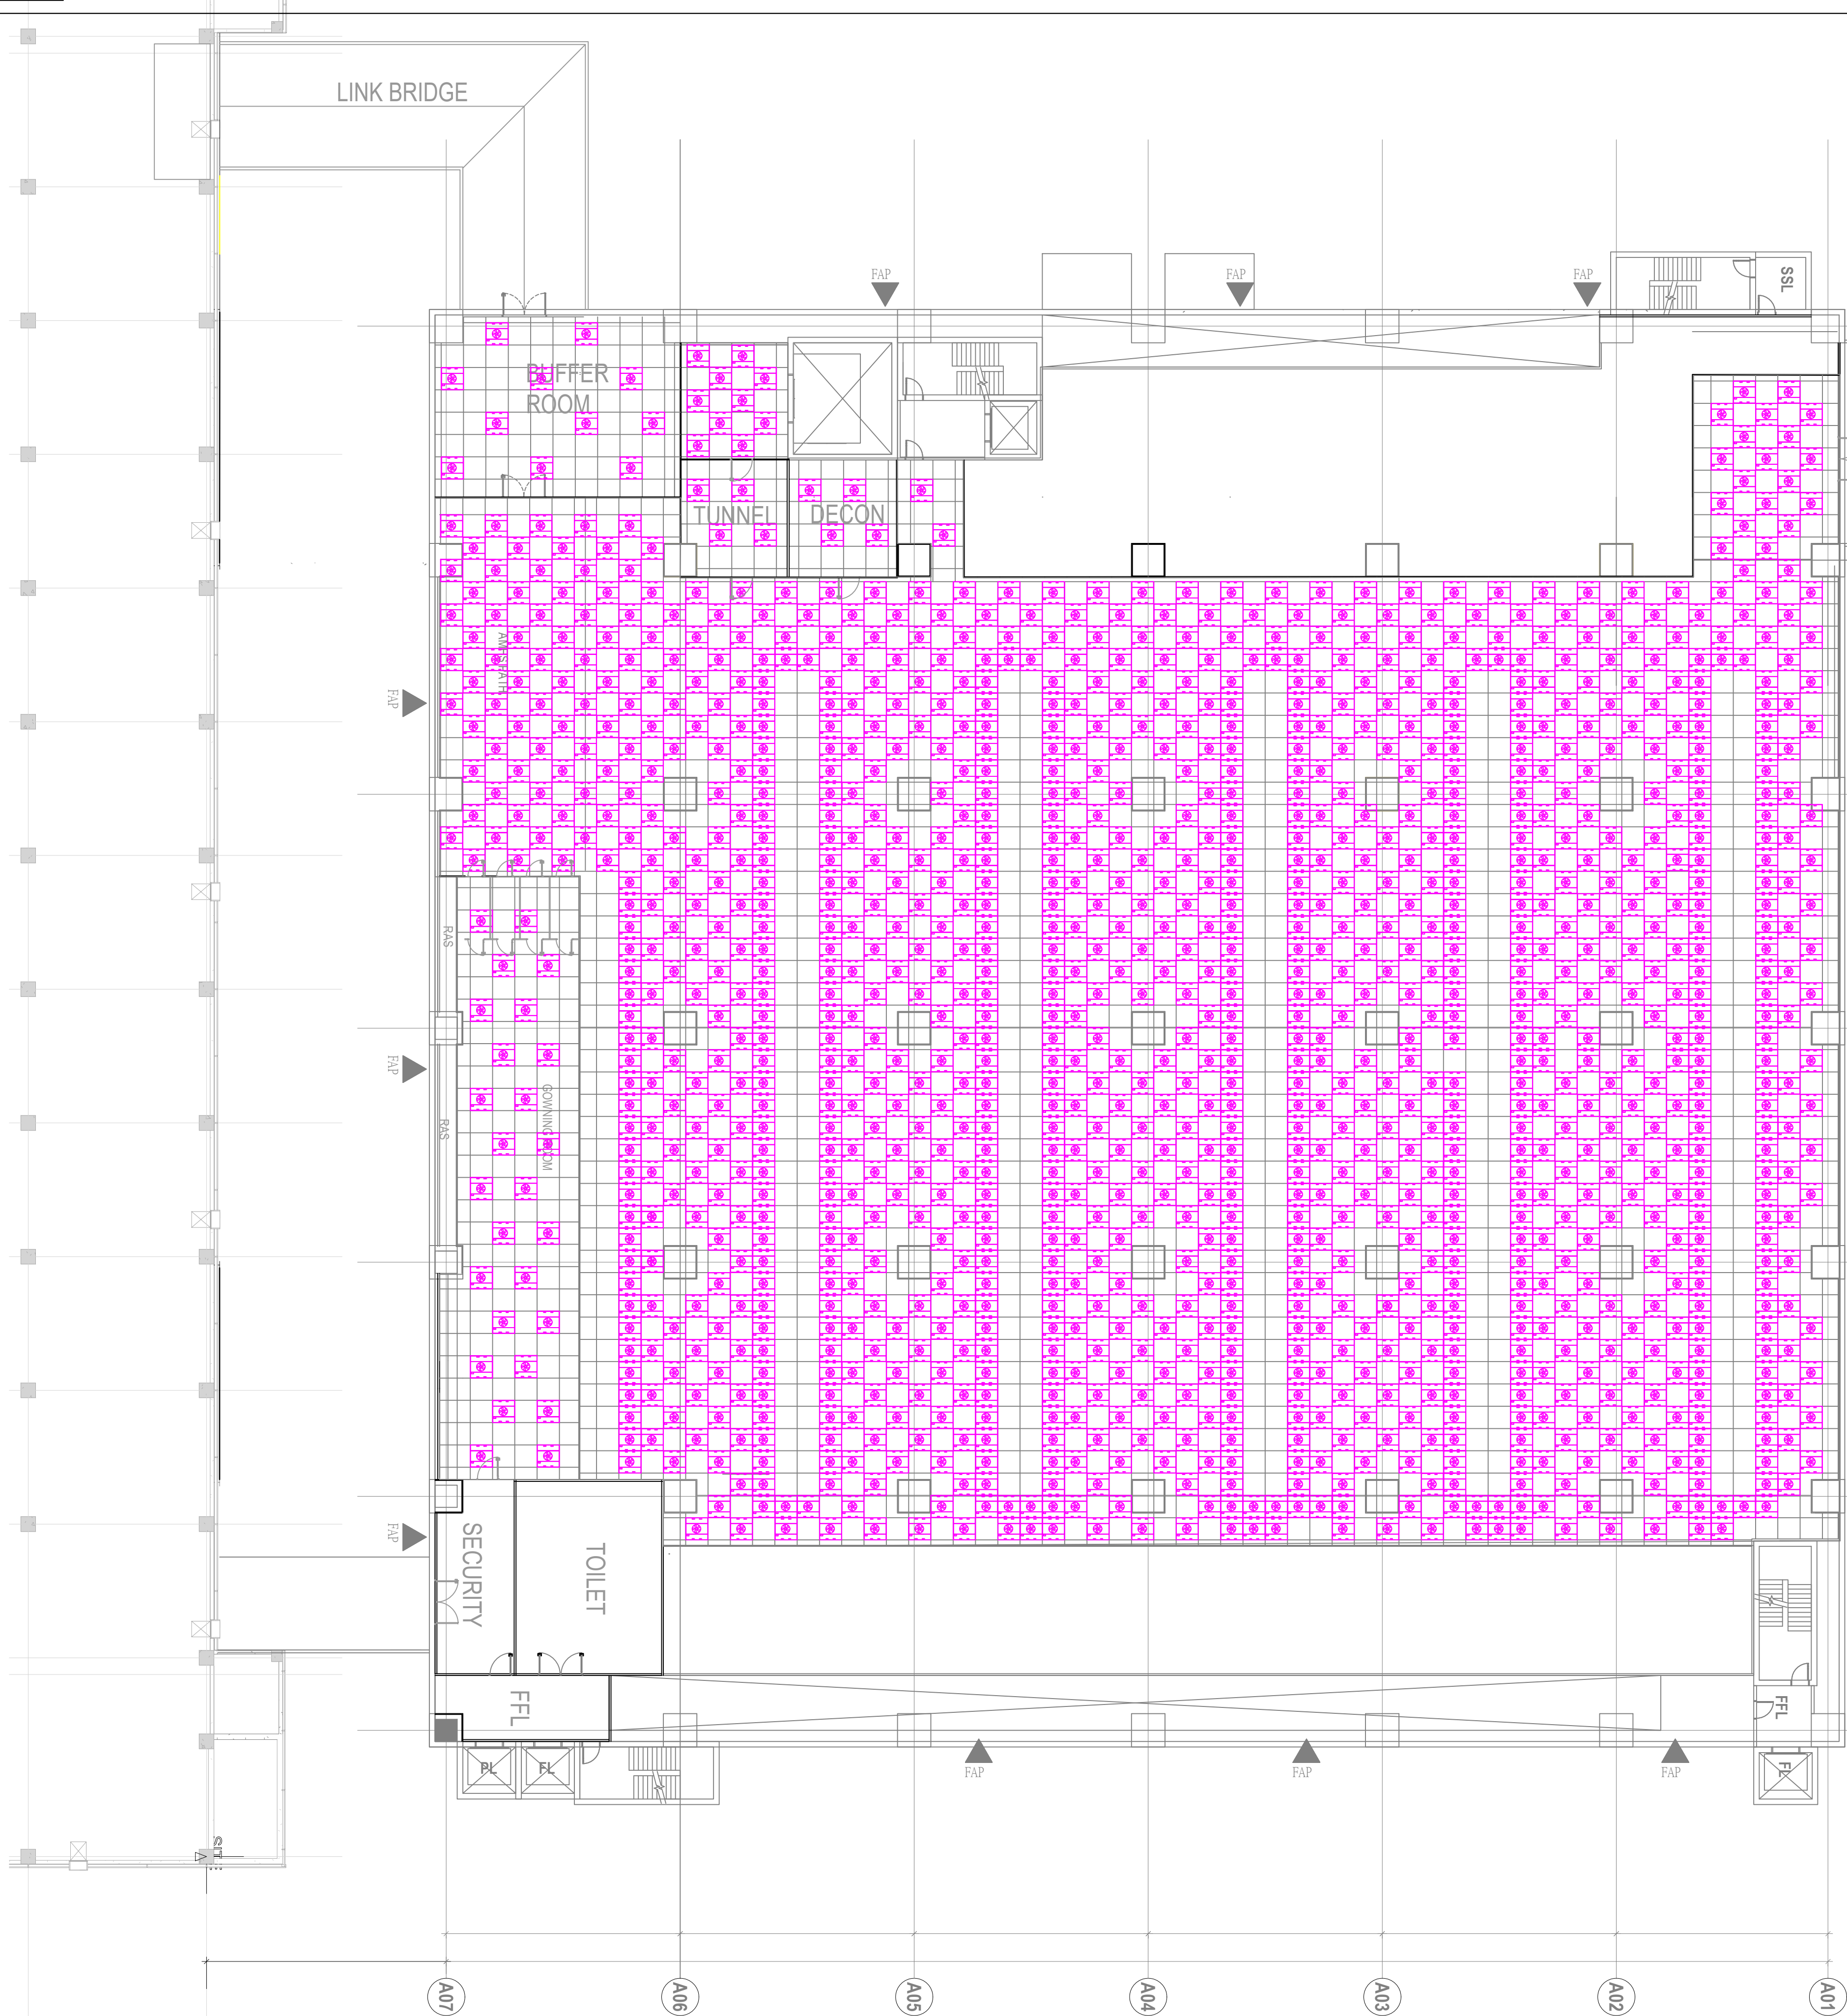

F10E1 L30 FFU LAYOUT SCALE 1:200

OWNER / DEVELOPER

ARCHITECTURAL CONSULTANT

CIVIL & STRUCTURAL CONSULTANT

MECHANICAL & ELECTRICAL CONSULTANT

DESIGN MANAGER

CTCI Singapore Pte. Ltd.

PROJECT ADDRESS

North Coast Drive, Singapore

KEY PLAN

Secret
R3
Level

SHEET PURPOSE

REV	DATE	DESCRIPTION Revisions	ISSUED BY

PROJECT TITLE

Micron F10E Probe Project

PROJECT PHASE

A&E

DRAWING TITLE

Floor Plan - FFU Layout F10E1 L30

DESIGNED : 設計者	DRAWN : 作者	CHECKED : 審圖員
DATE : 02/11/26	JOB NO. :	SCALE :
Micron DRAWING NO. : F01-F10E-LAY-F10E1-03-k-126	REV	
CTCI DRAWING NO. :	0A	
Reference Model		
CTCI	SHEET: 1 OF 1	SIZE A1