


CONSENT NOTICE: THE CONTENT OF THIS DOCUMENT IS ESSENTIAL INFORMATION AND OWNED BY MICRON CORPORATION AND IS PROTECTED BY COPYRIGHT LAWS AND RELATED JURISDICTIONS. ONLY EMPLOYEES OF MICRON ARE ALLOWED TO ACCESS AND USE THIS ESSENTIAL INFORMATION WITHIN THE WORK SCOPE UNDER THEIR SPECIFIC AND RESPECTIVE DUTIES AND OBLIGATIONS REQUIRED BY AGREEMENT. WHICH IS NOT ALLOWED TO COPY, REPRODUCE, DISTRIBUTE, PUBLISH OR DISCLOSE IN WHOLE OR IN PART TO ANY OTHER PARTY WITHOUT CTCS PRIOR AND WRITTEN CONSENT.

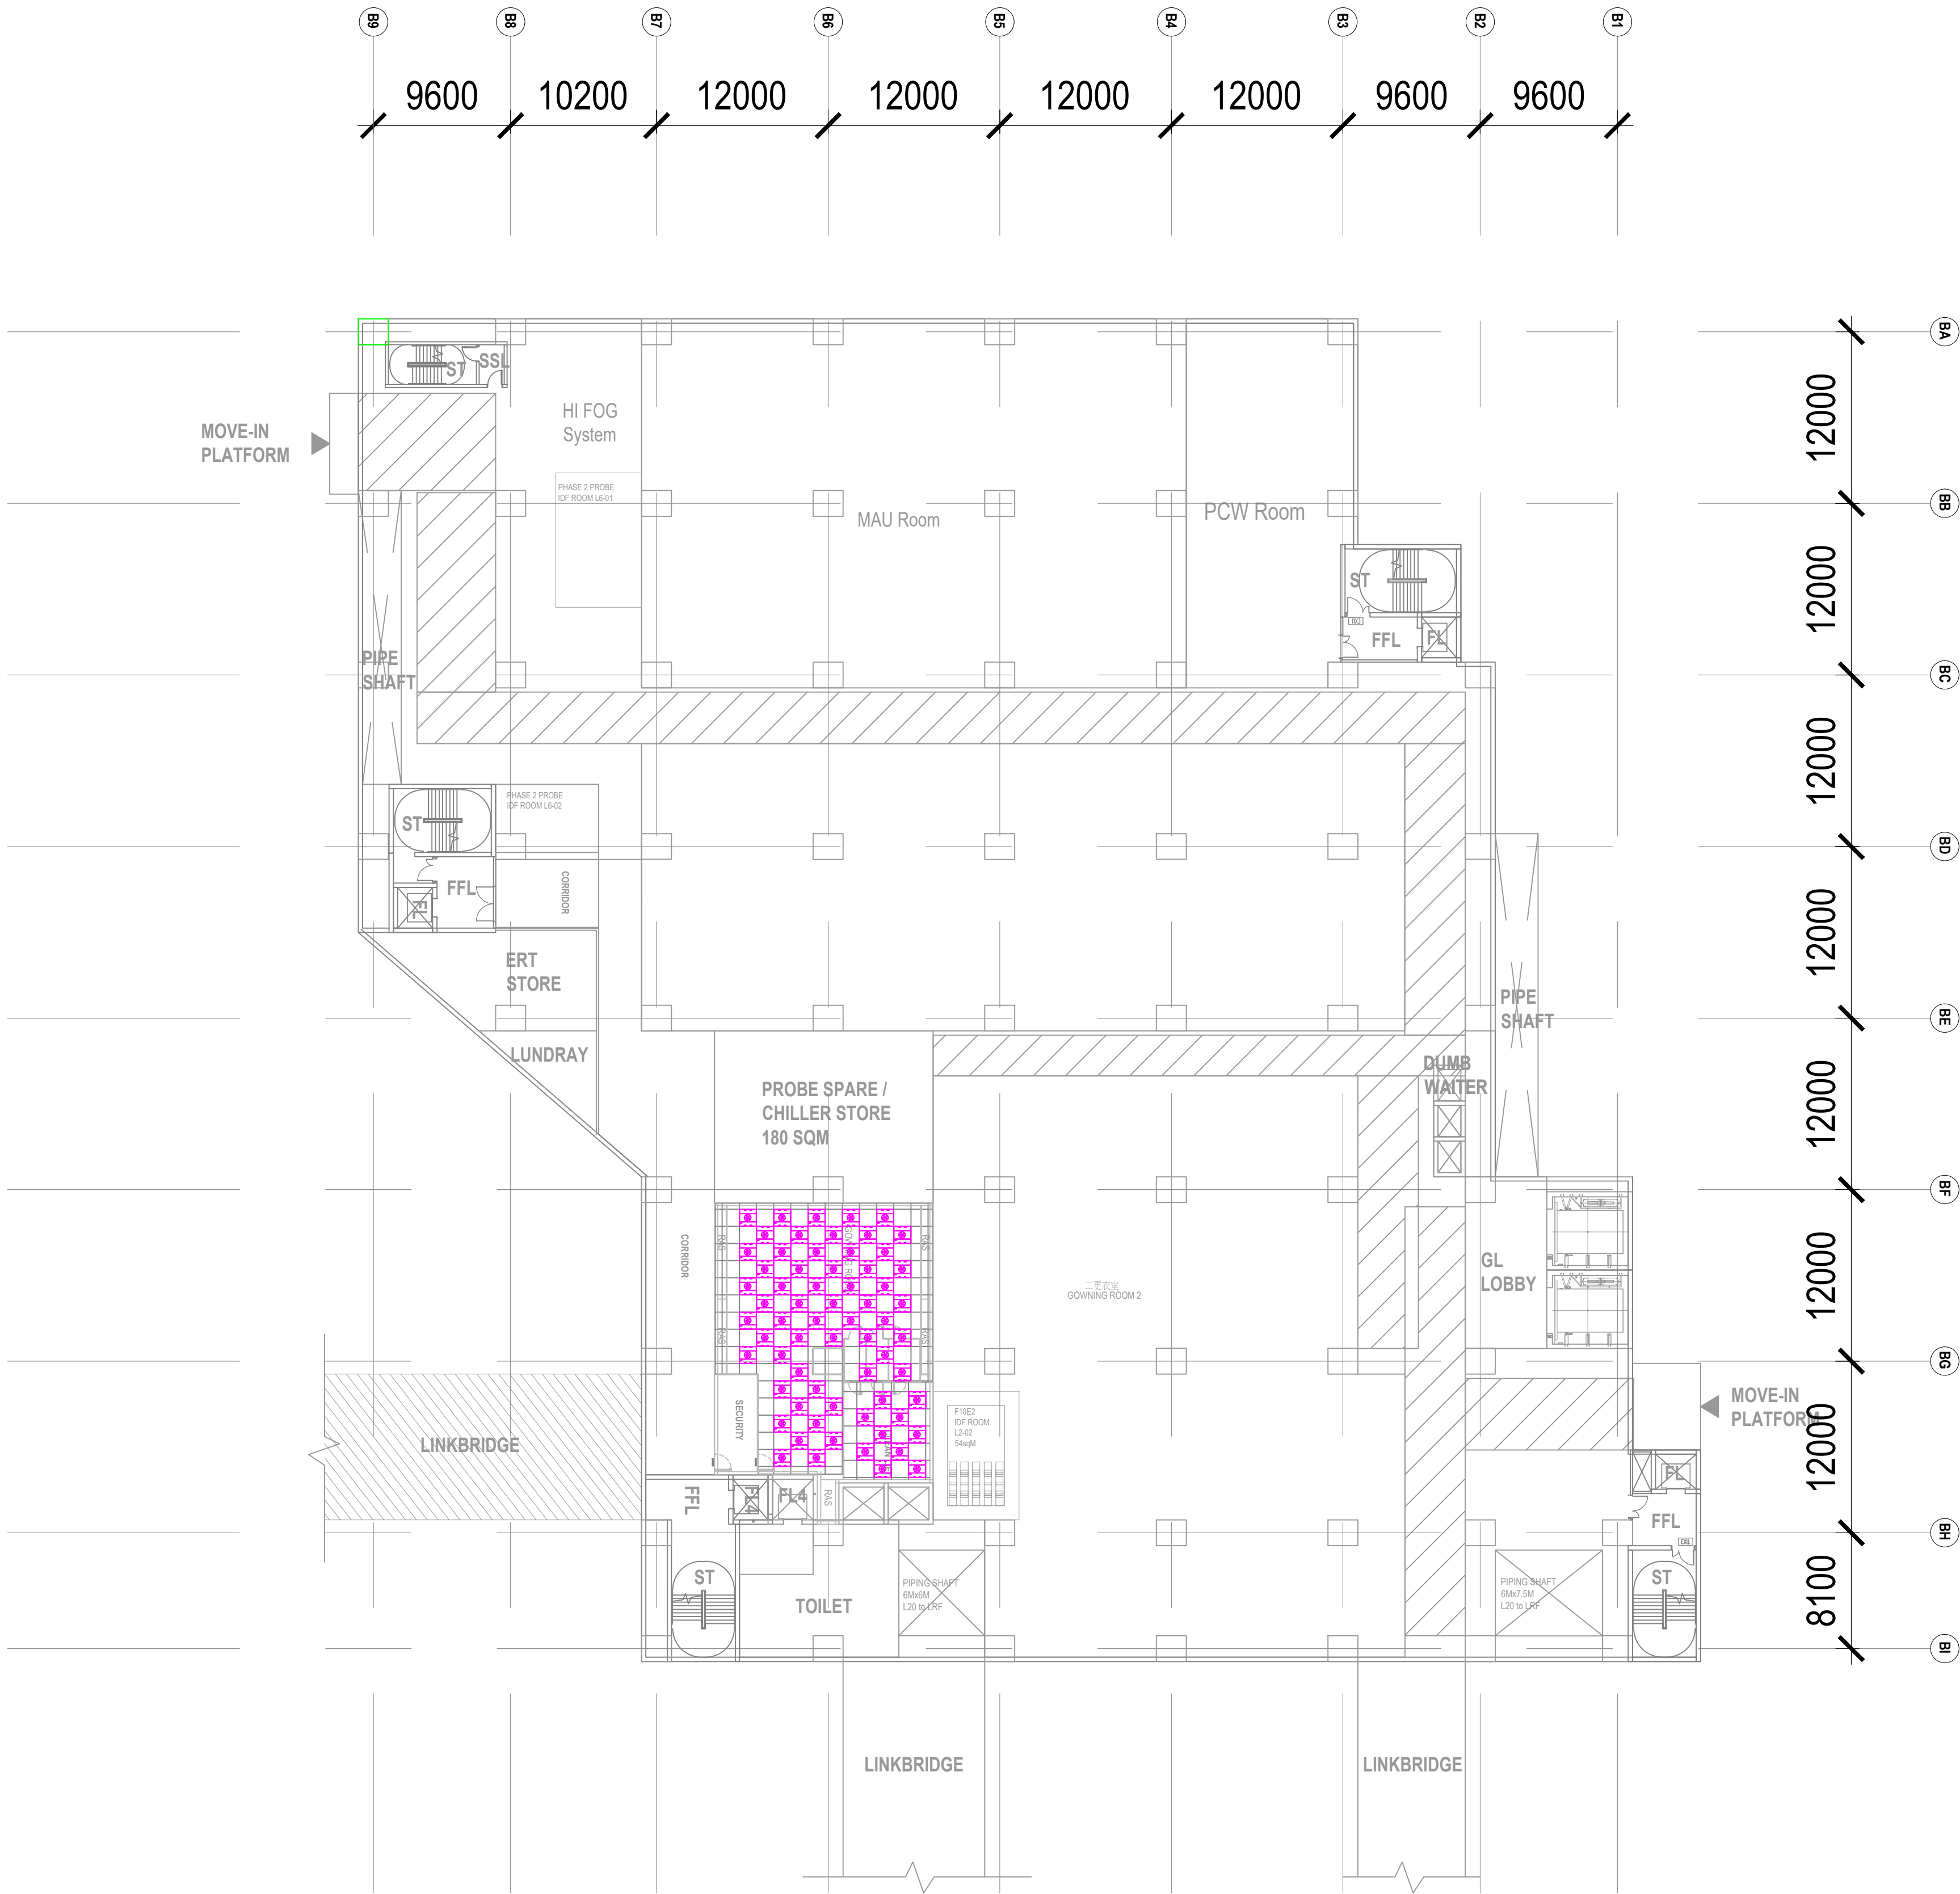

F10E2 L20 FFU LAYOUT SCALE 1:300

OWNER / DEVELOPER

ARCHITECTURAL CONSULTANT

CIVIL & STRUCTURAL CONSULTANT

MECHANICAL & ELECTRICAL CONSULTANT

DESIGN MANAGER

CTCI Singapore Pte. Ltd.

PROJECT ADDRESS

North Coast Drive, Singapore

KEY PLAN

Secret

R3

Level

SHEET PURPOSE

REV	DATE	DESCRIPTION	ISSUED BY
		Revisions	

PROJECT TITLE

Micron F10E Probe Project

PROJECT PHASE

A&E

DRAWING TITLE

Floor Plan - FFU Layout F10E2 L20

DESIGNED :	設計者	DRAWN :	作者	CHECKED :	審圖員
DATE :	02/11/26	JOB NO. :		SCALE :	
Micron	F01-F10E-LAY-F10E2-02-K-126				REV
DRAWING NO.					0A
CTCI					
DRAWING NO.					
Reference Model					
CTCI	SHEET: 1 OF 1				SIZE: A1