


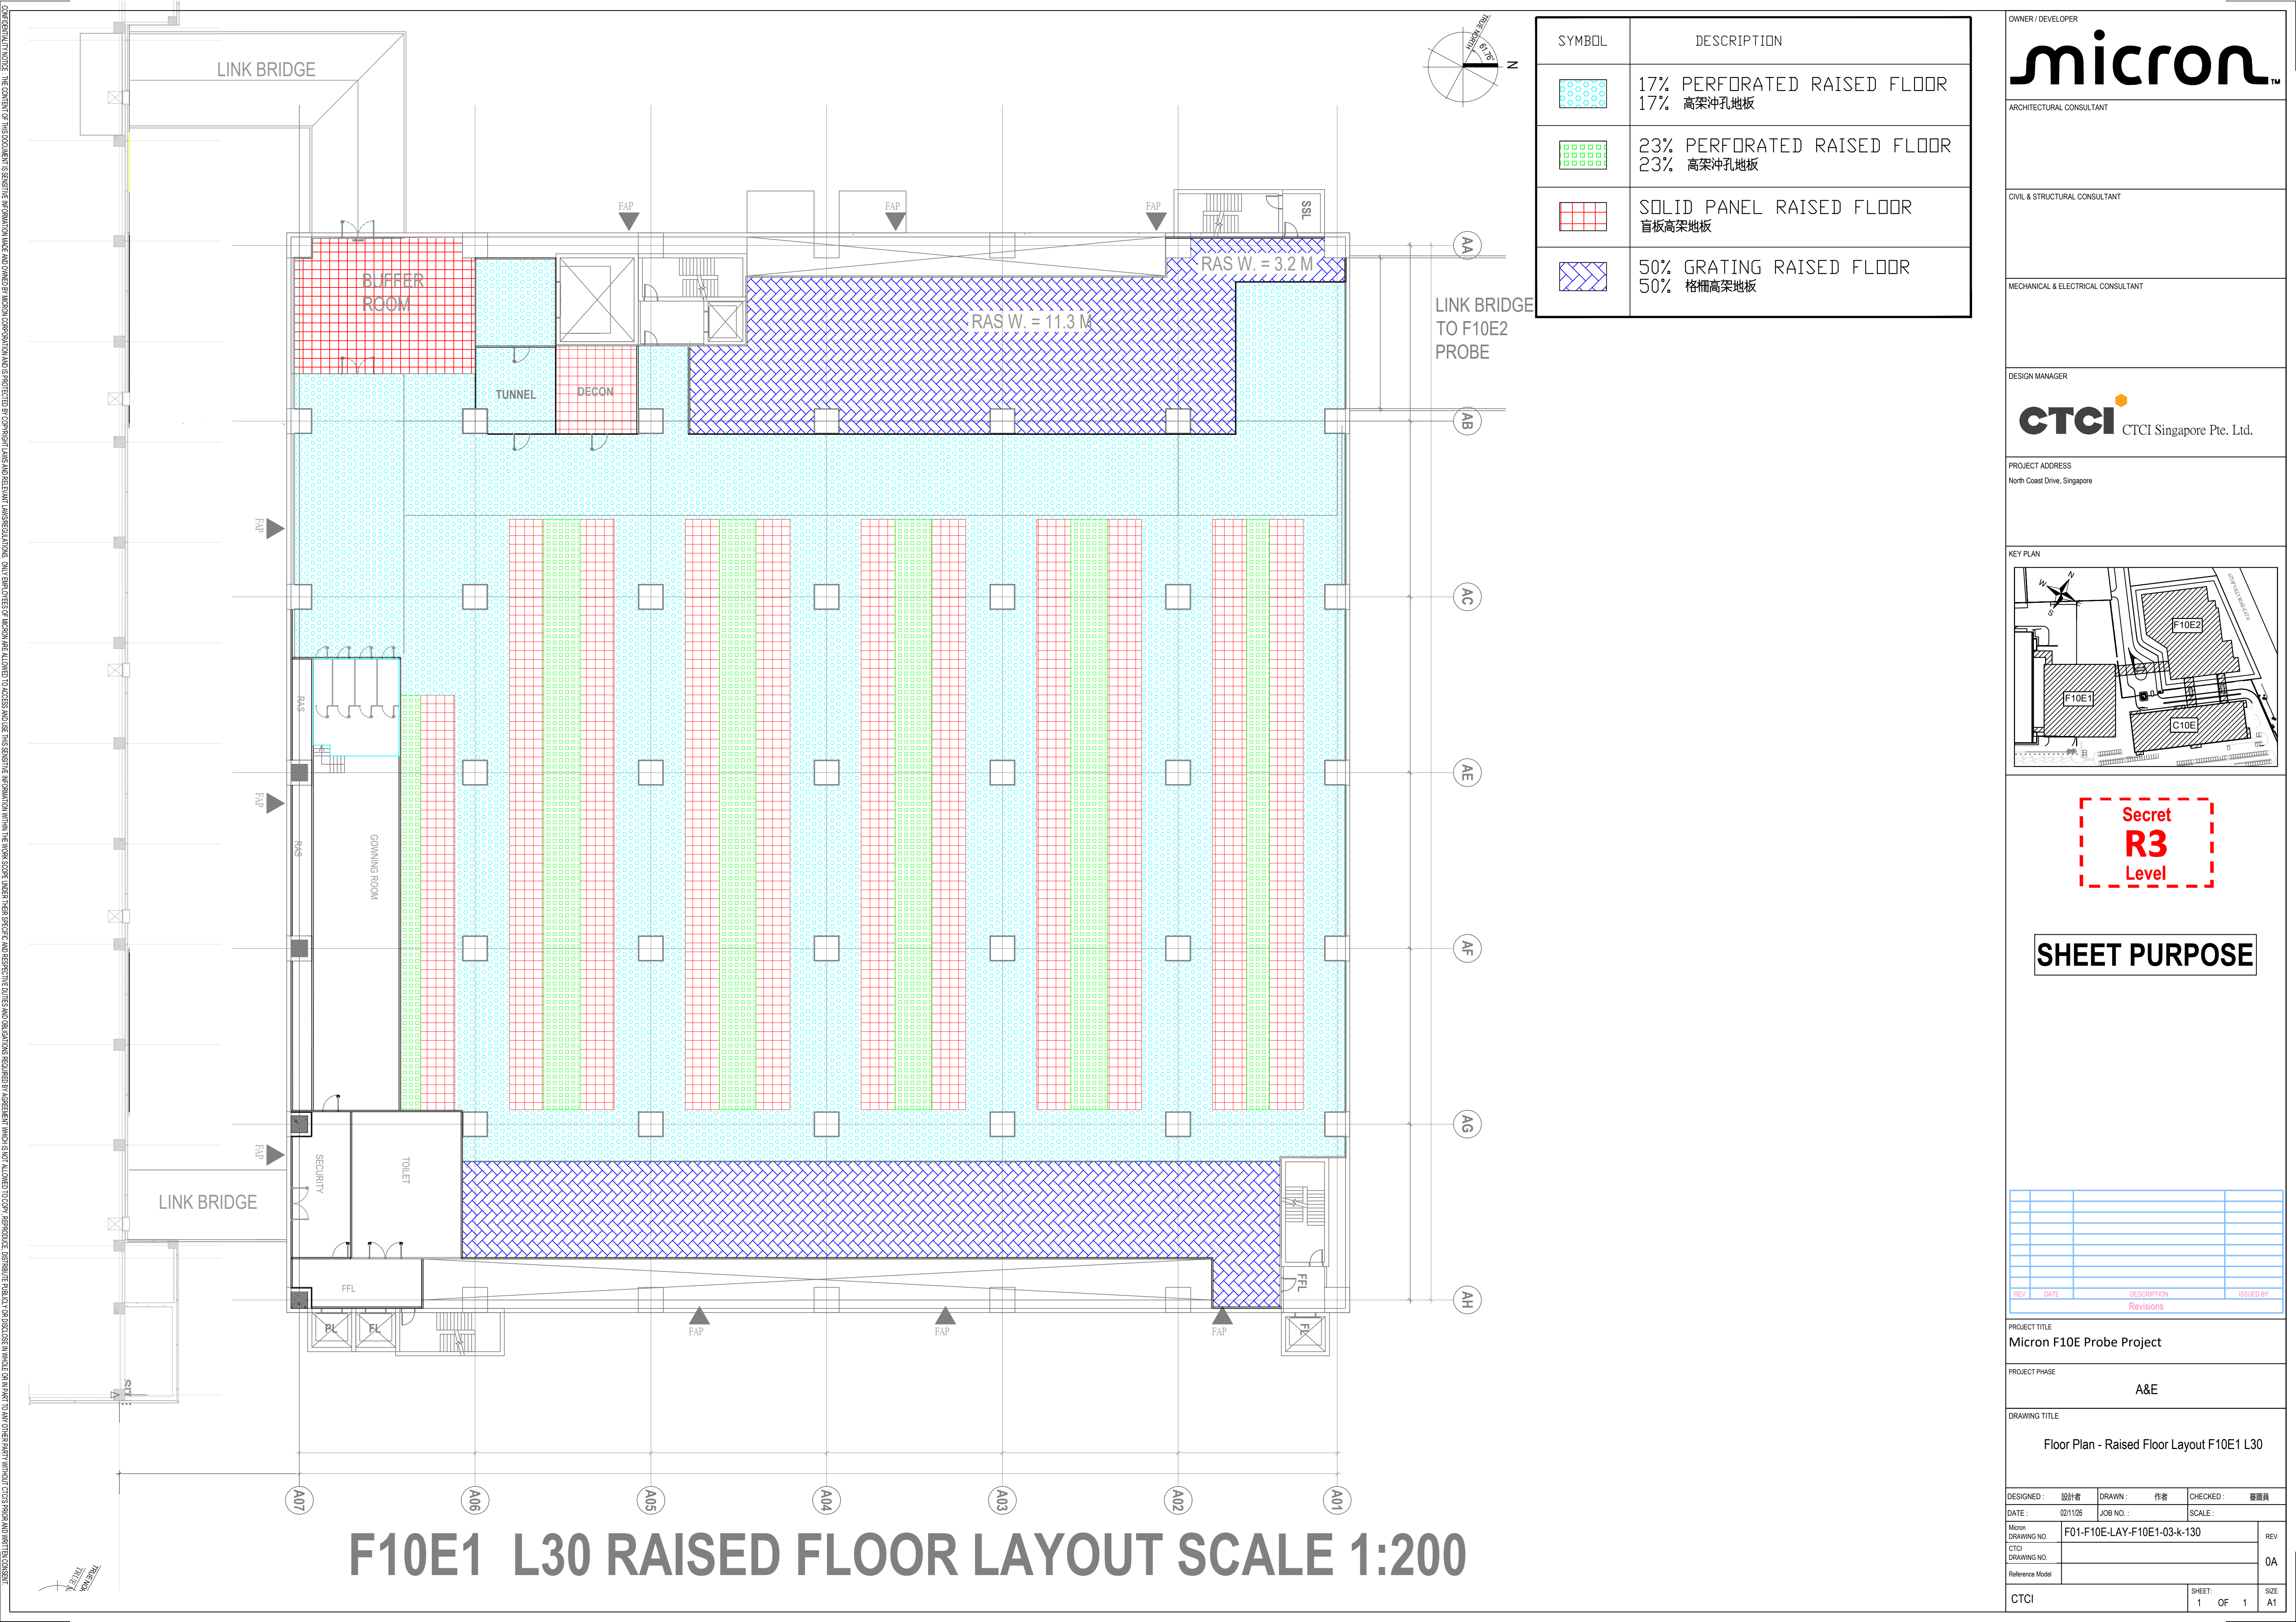

SYMBOL	DESCRIPTION
	17% PERFORATED RAISED FLOOR 17% 高架冲孔地板
	23% PERFORATED RAISED FLOOR 23% 高架冲孔地板
	SOLID PANEL RAISED FLOOR 盲板高架地板
	50% GRATING RAISED FLOOR 50% 格栅高架地板

OWNER / DEVELOPER
micron™

ARCHITECTURAL CONSULTANT

CIVIL & STRUCTURAL CONSULTANT

MECHANICAL & ELECTRICAL CONSULTANT


DESIGN MANAGER

CTCI CTCI Singapore Pte. Ltd.

PROJECT ADDRESS

North Coast Drive, Singapore

KEY PLAN

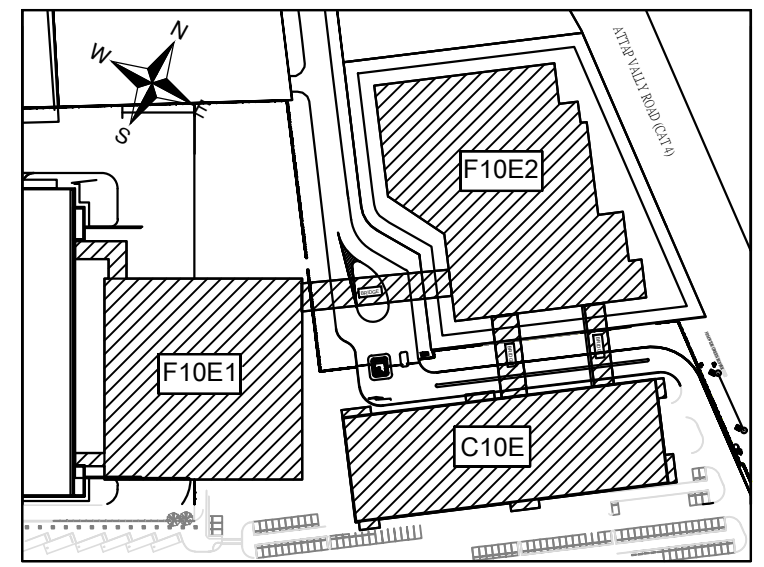

Secret
R3
Level

SHEET PURPOSE

REV	DATE	DESCRIPTION Revisions	ISSUED BY

PROJECT TITLE
Micron F10E Probe Project

PROJECT PHASE
A&E

DRAWING TITLE
Floor Plan - Raised Floor Layout F10E1 L30

DESIGNED : 設計者	DRAWN : 作者	CHECKED : 審圖員
DATE : 02/11/26	JOB NO. :	SCALE :
Micron DRAWING NO. : F01-F10E-LAY-F10E1-03-k-130	REV	
CTCI DRAWING NO. :	0A	
Reference Model	SHEET: 1 OF 1	
CTCI	SIZE A1	